




Easy Farming
AGRIPROM
total cow comfort

PROJECTNR.	DUT001-004
BLADNUMMER	B.02
OPDRACHTGEVER	Agriprom Nieuwleusen
PROJECTLEIDER	
TEKENAAR	
DATUM	05-08-2019
GEWIJZIGD	SCHAAL
A	
B	
C	
D	
	FORMAT A1




voortgang

 







Easy Farming




AGRIPRO







total cow comfort

   

 

 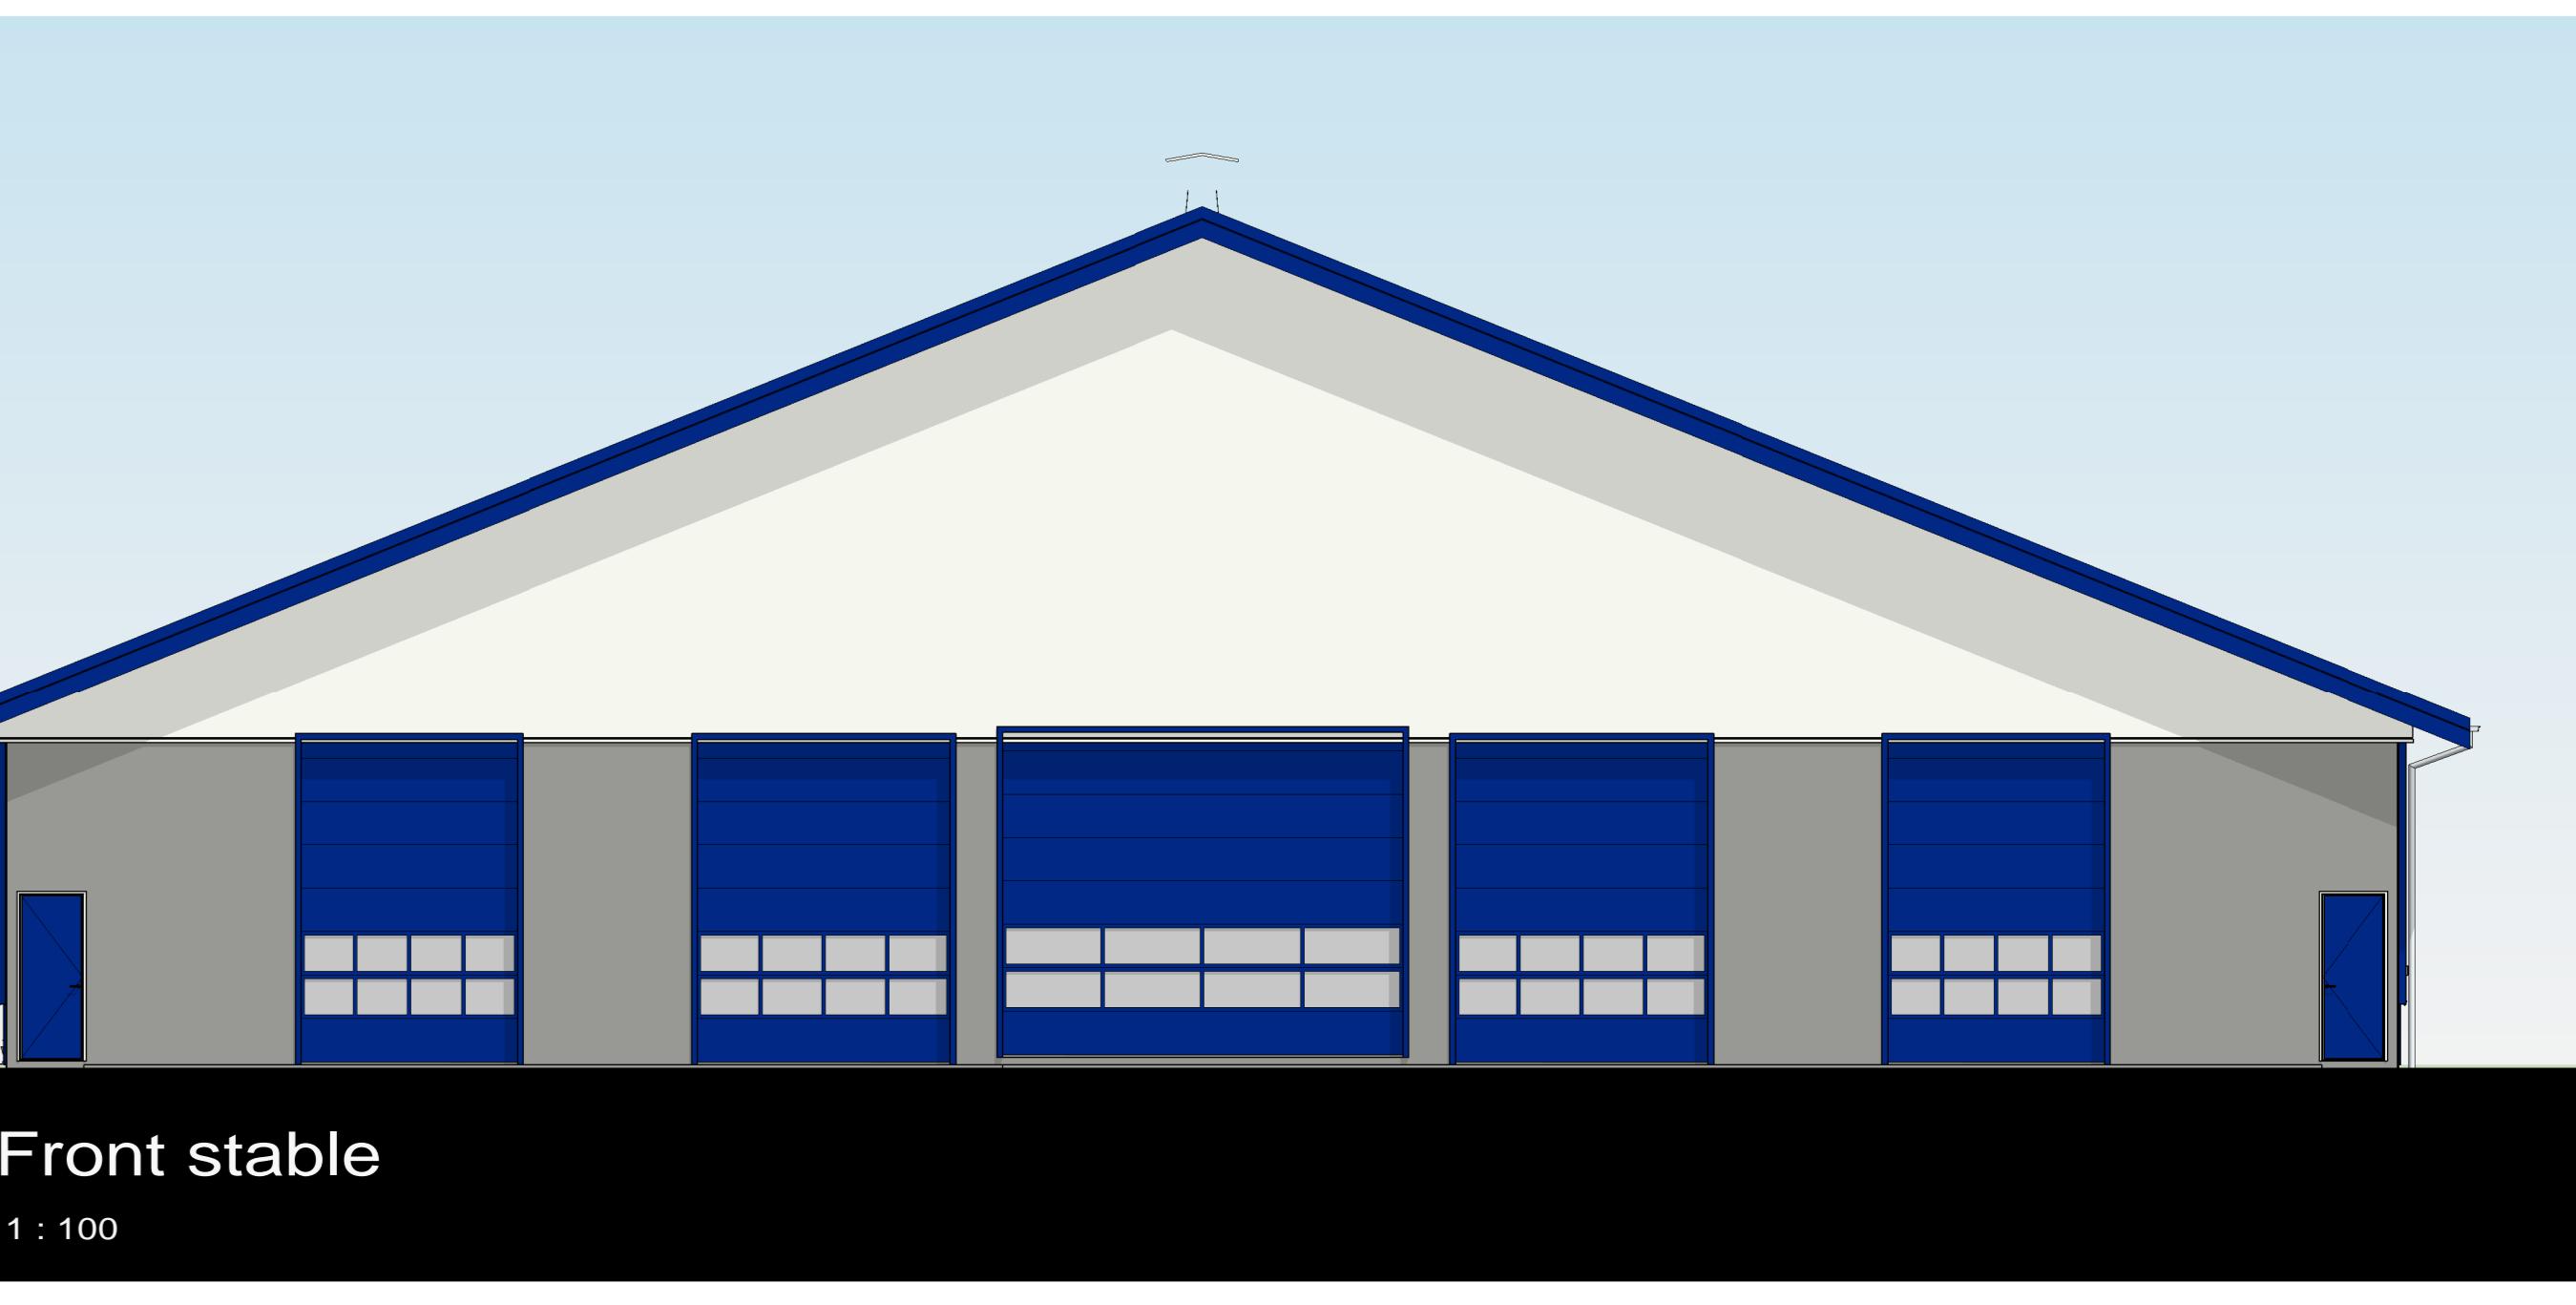 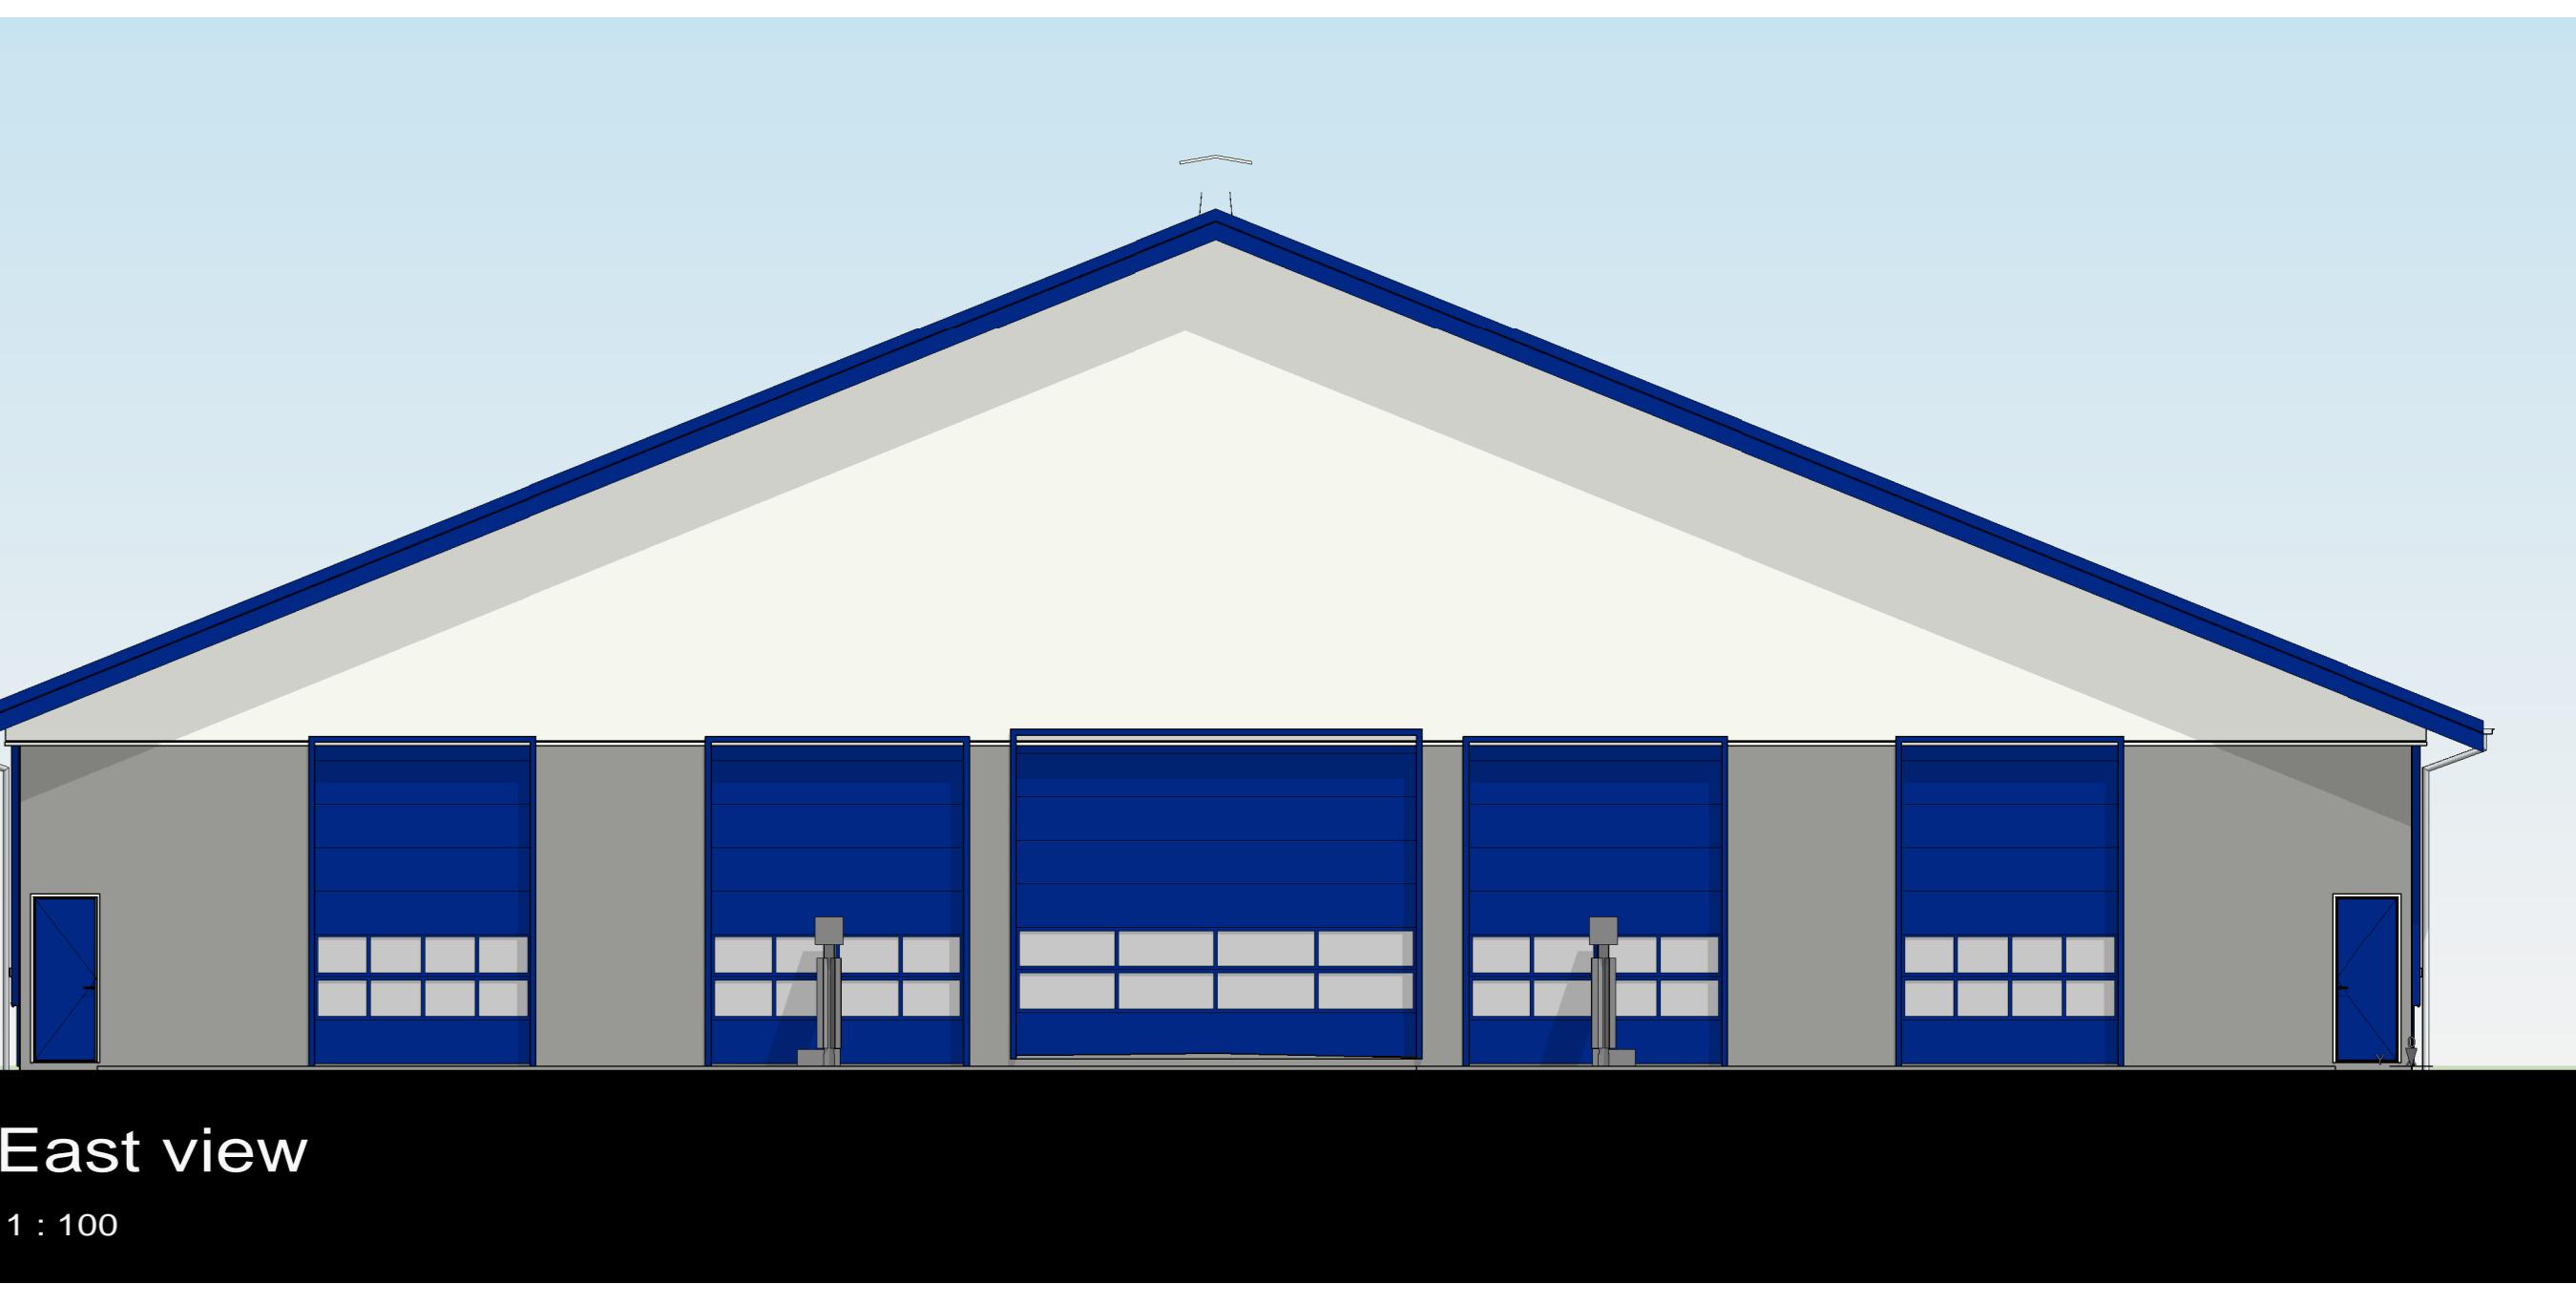 

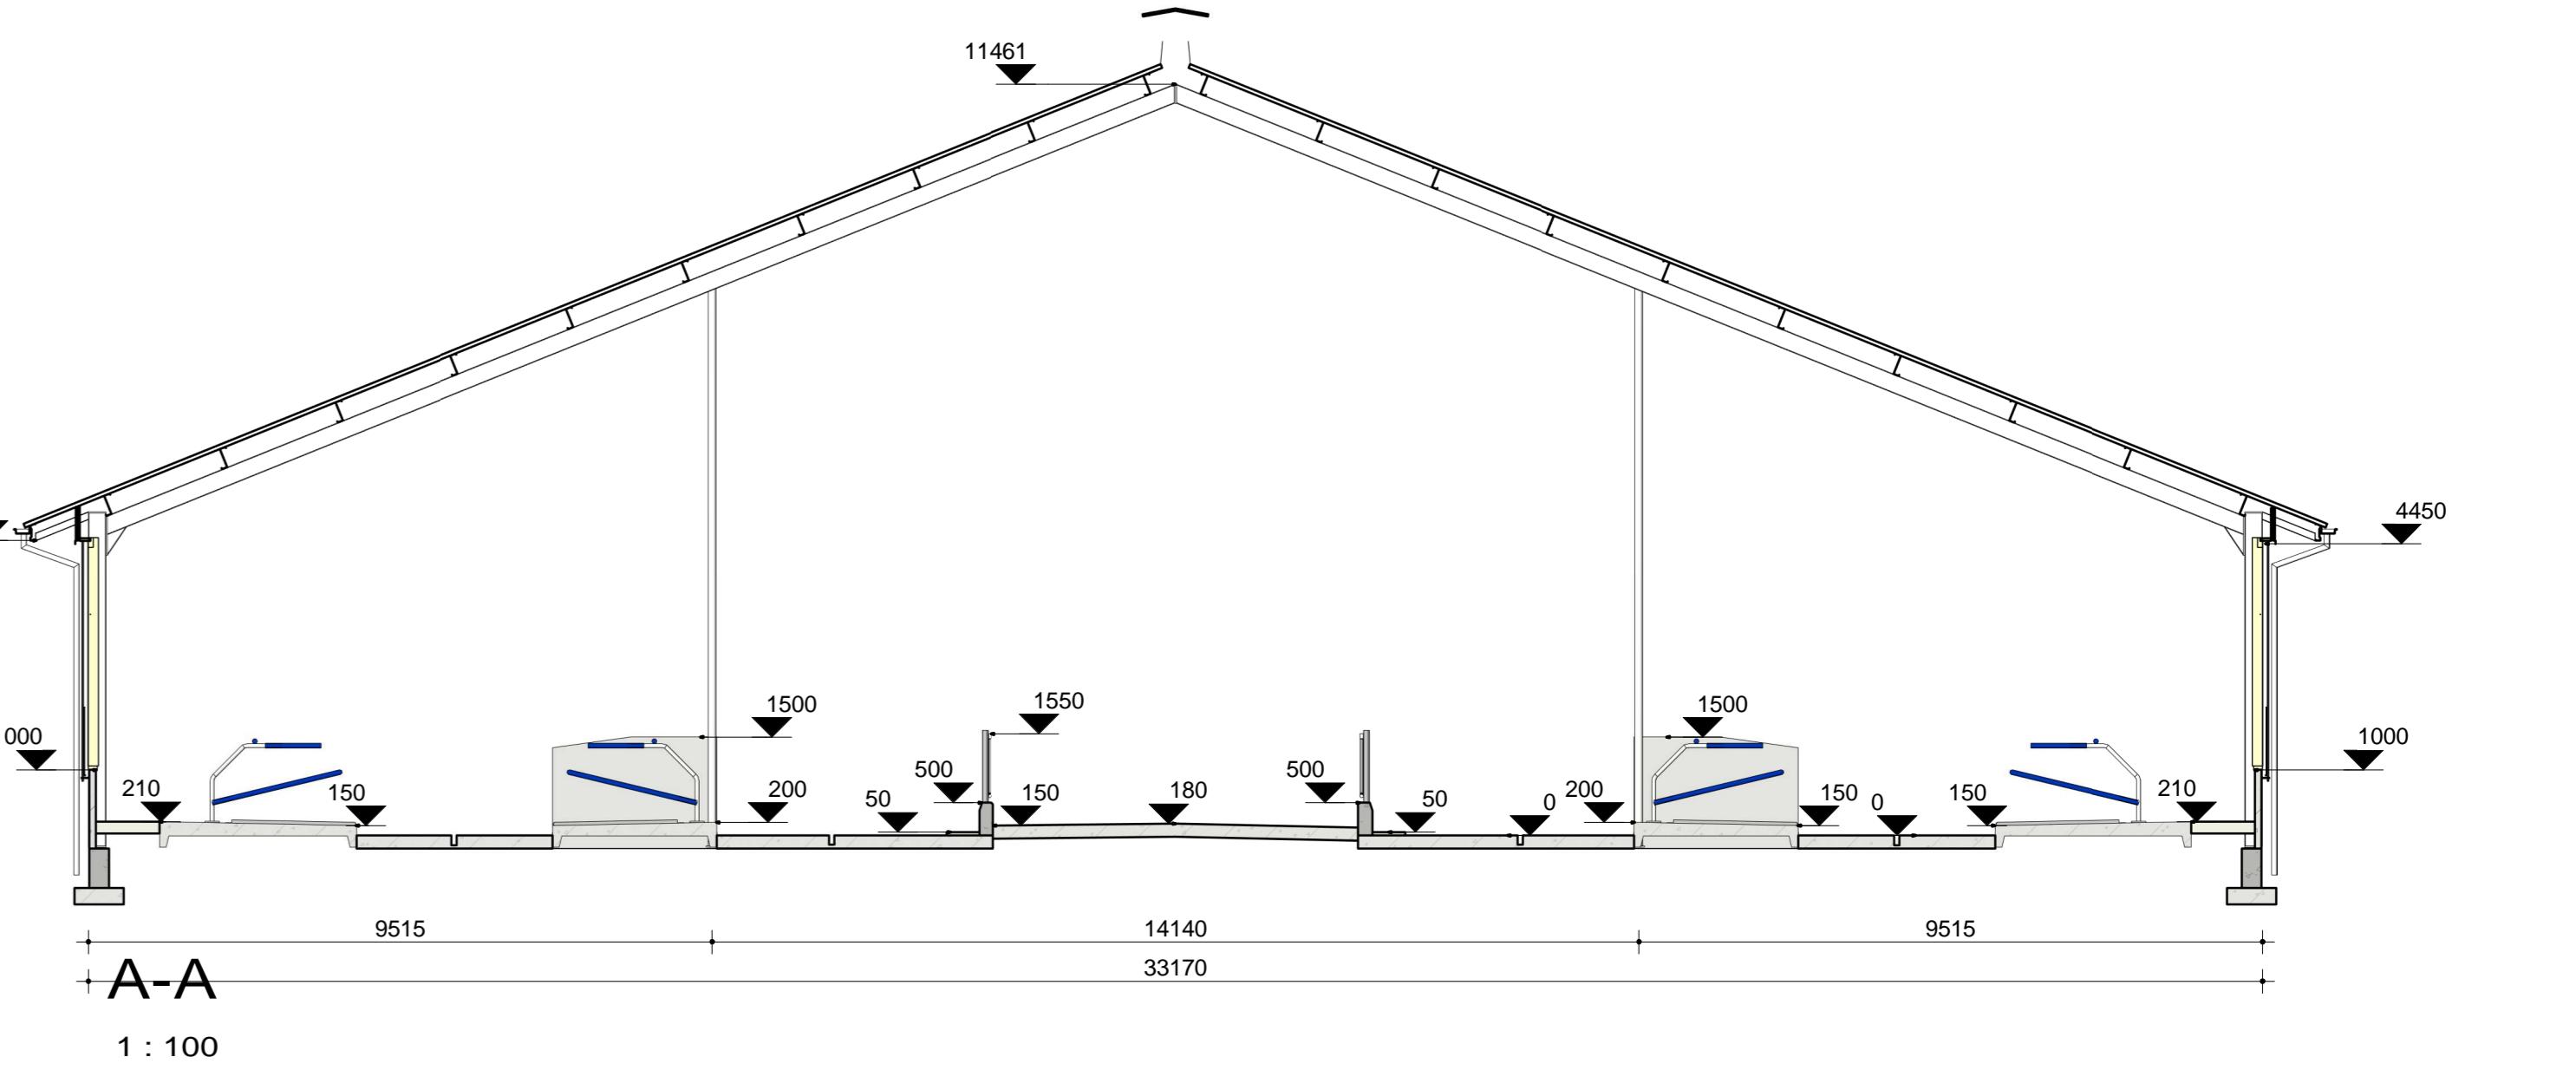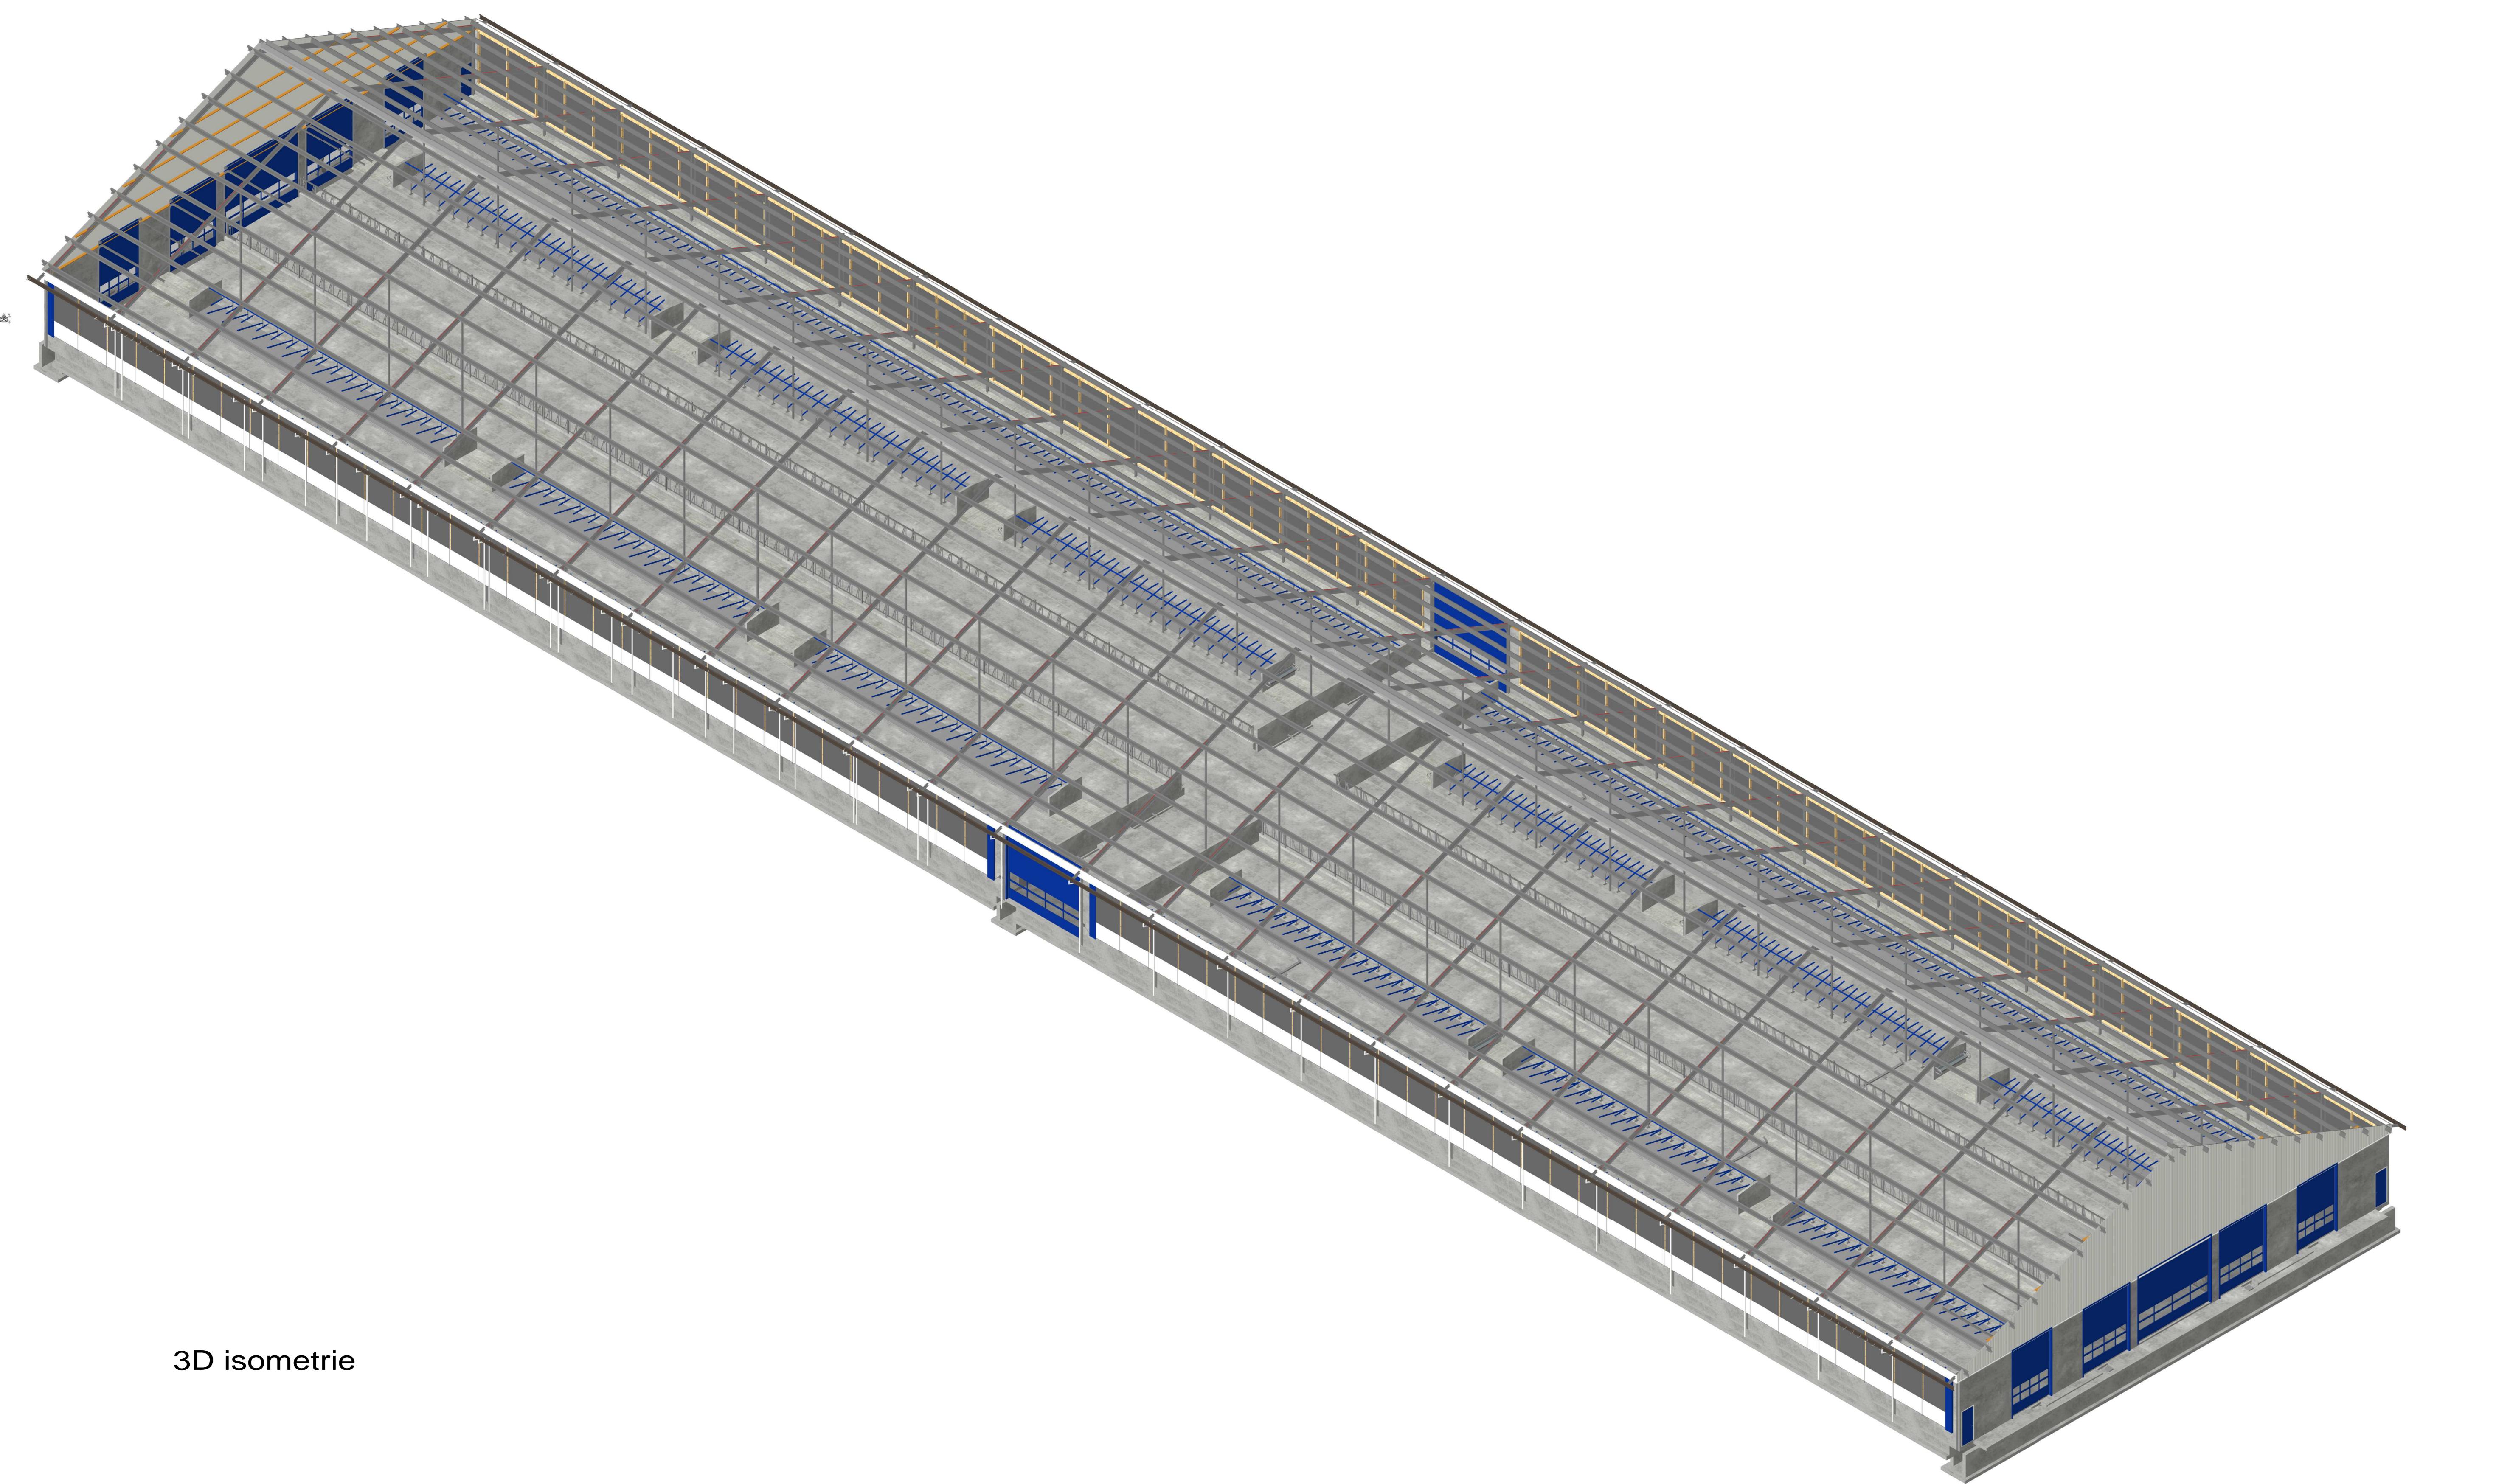 

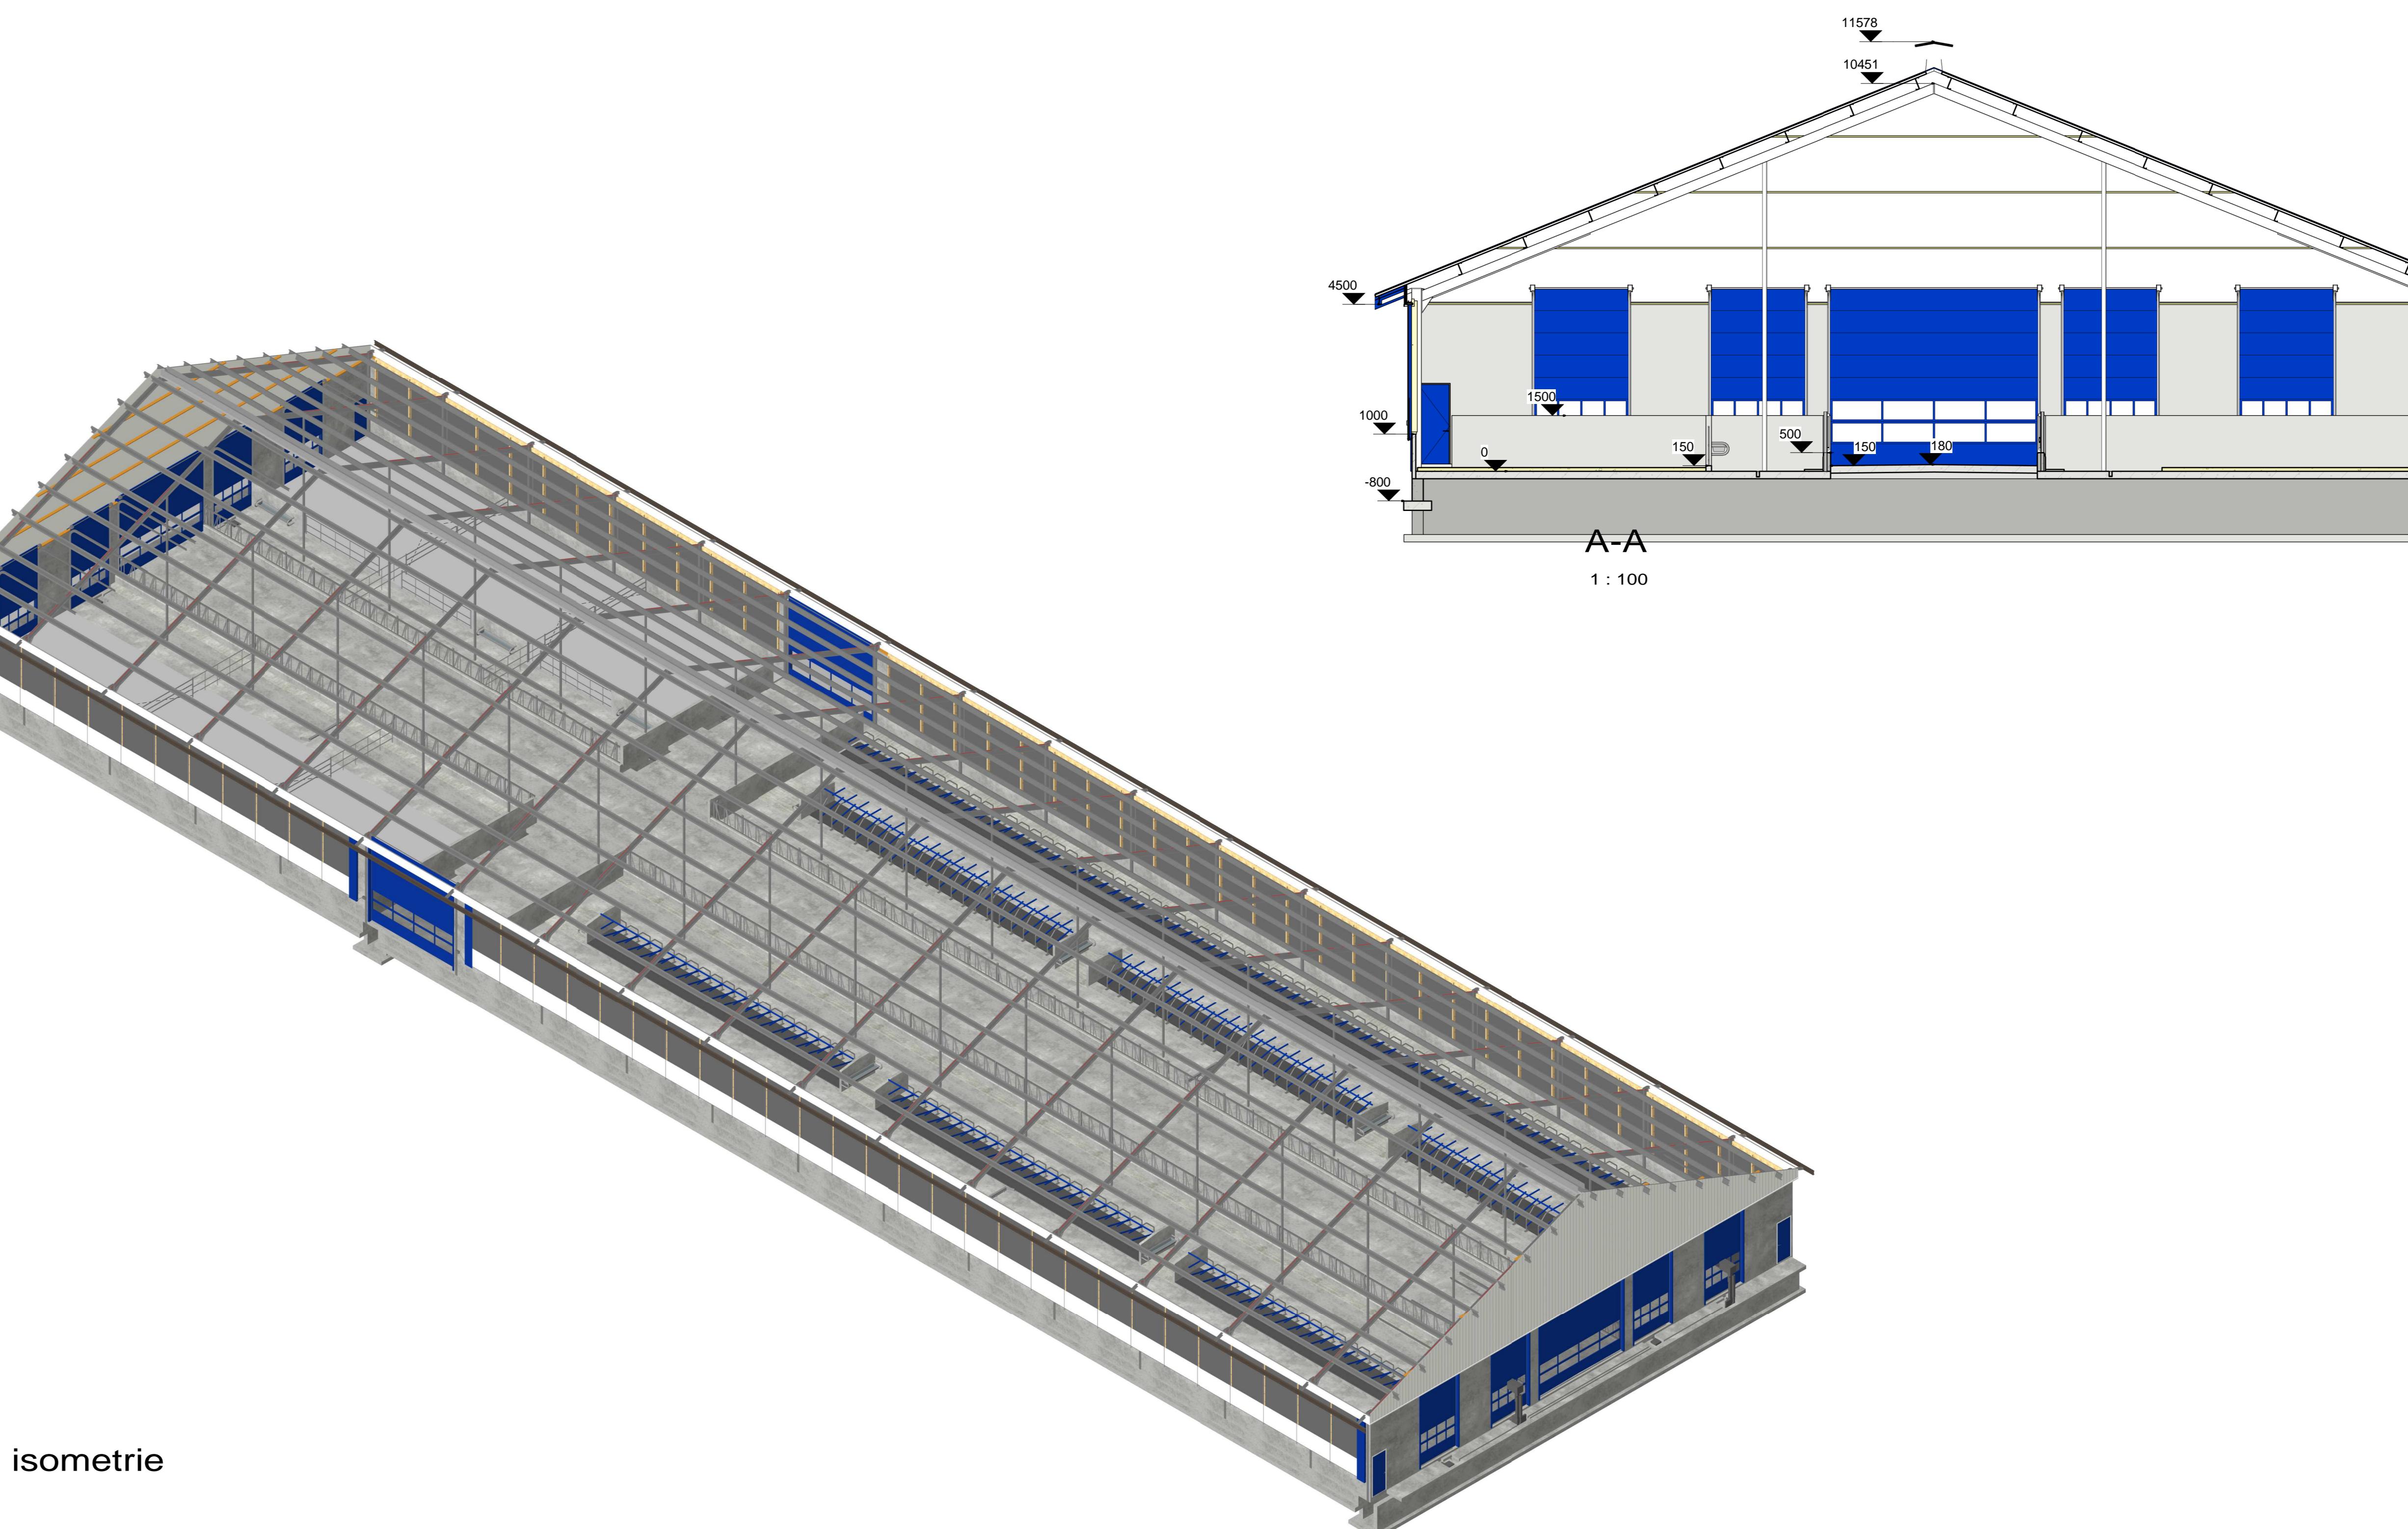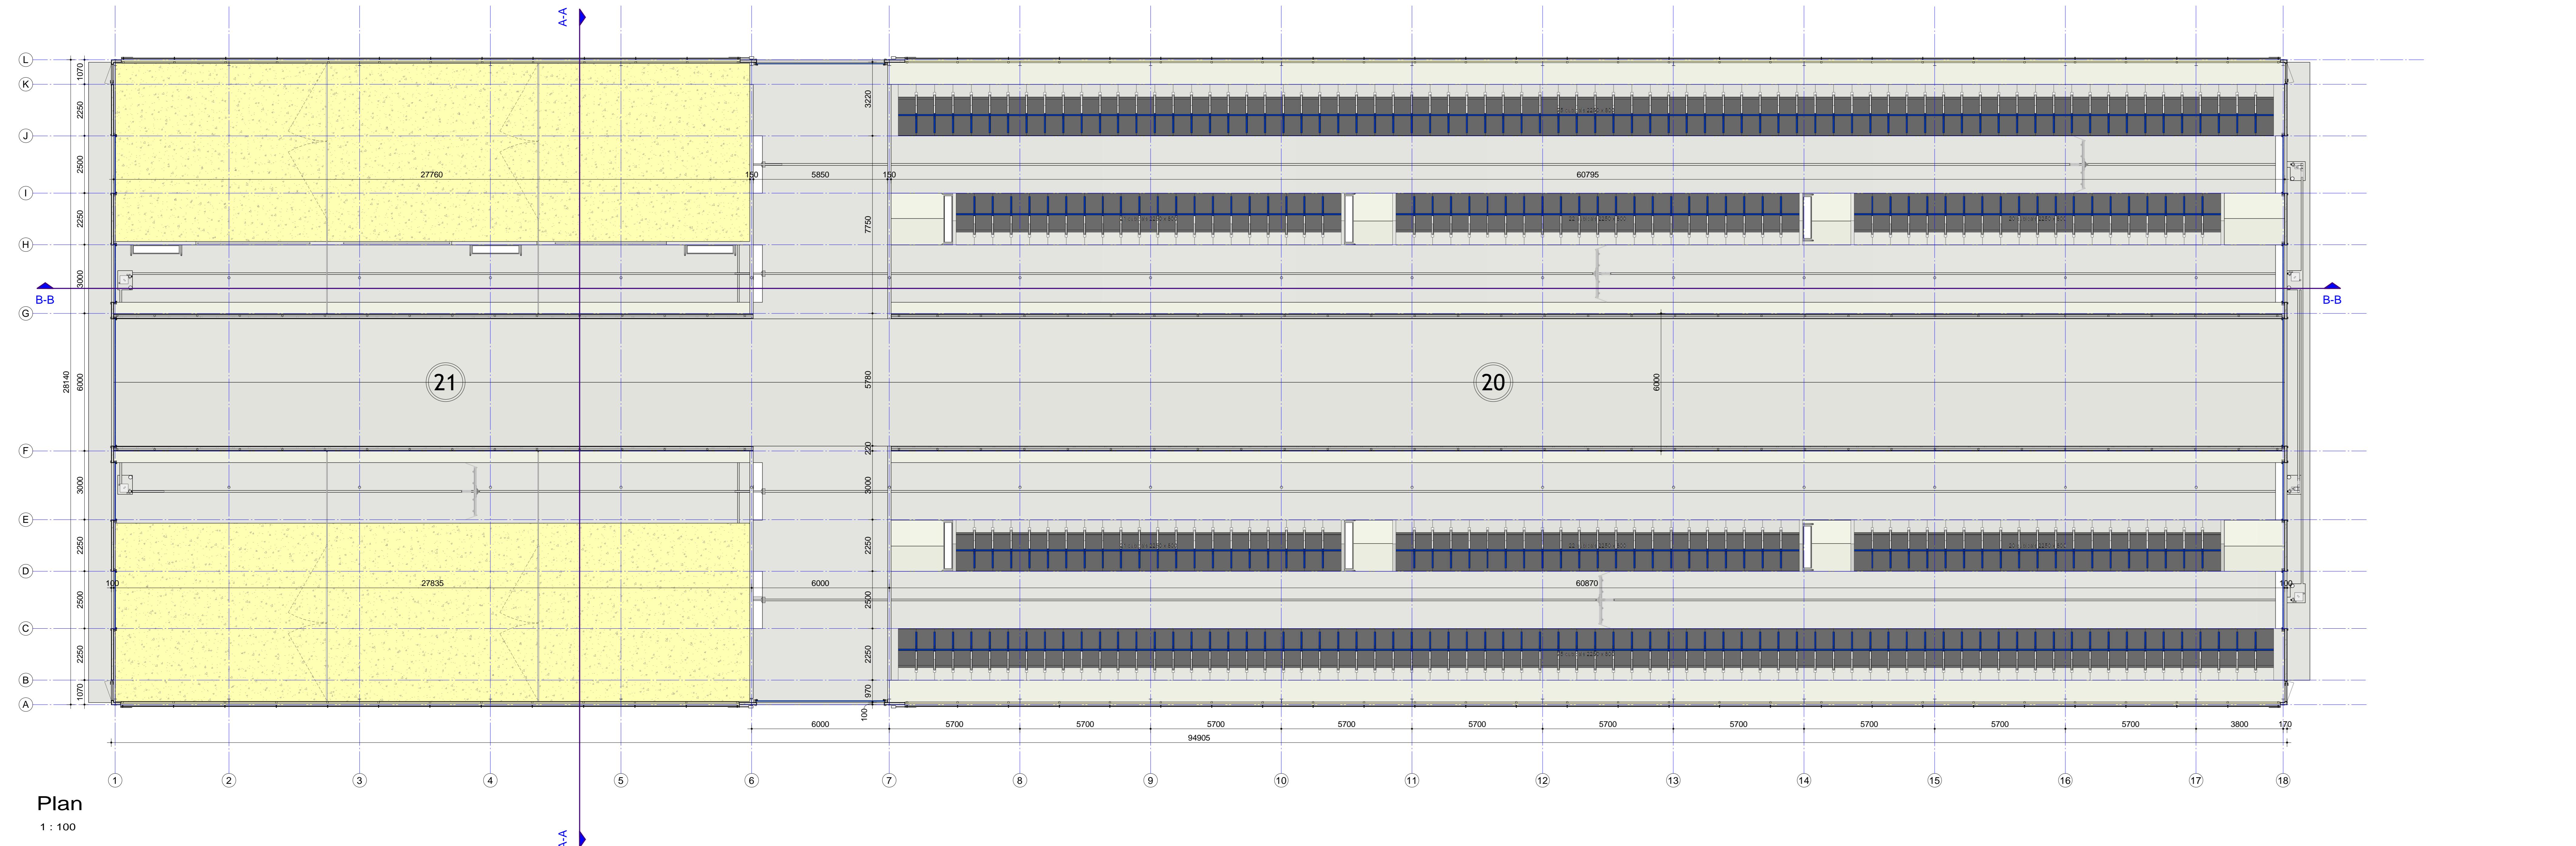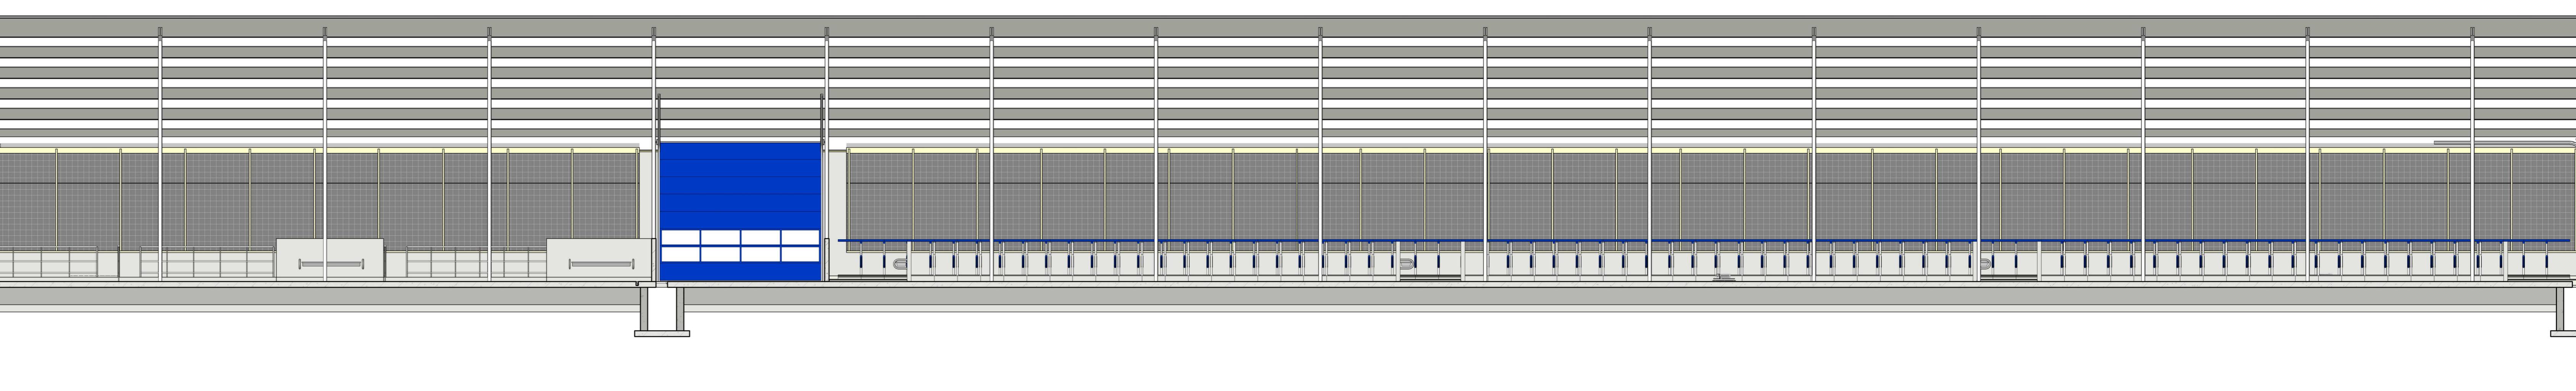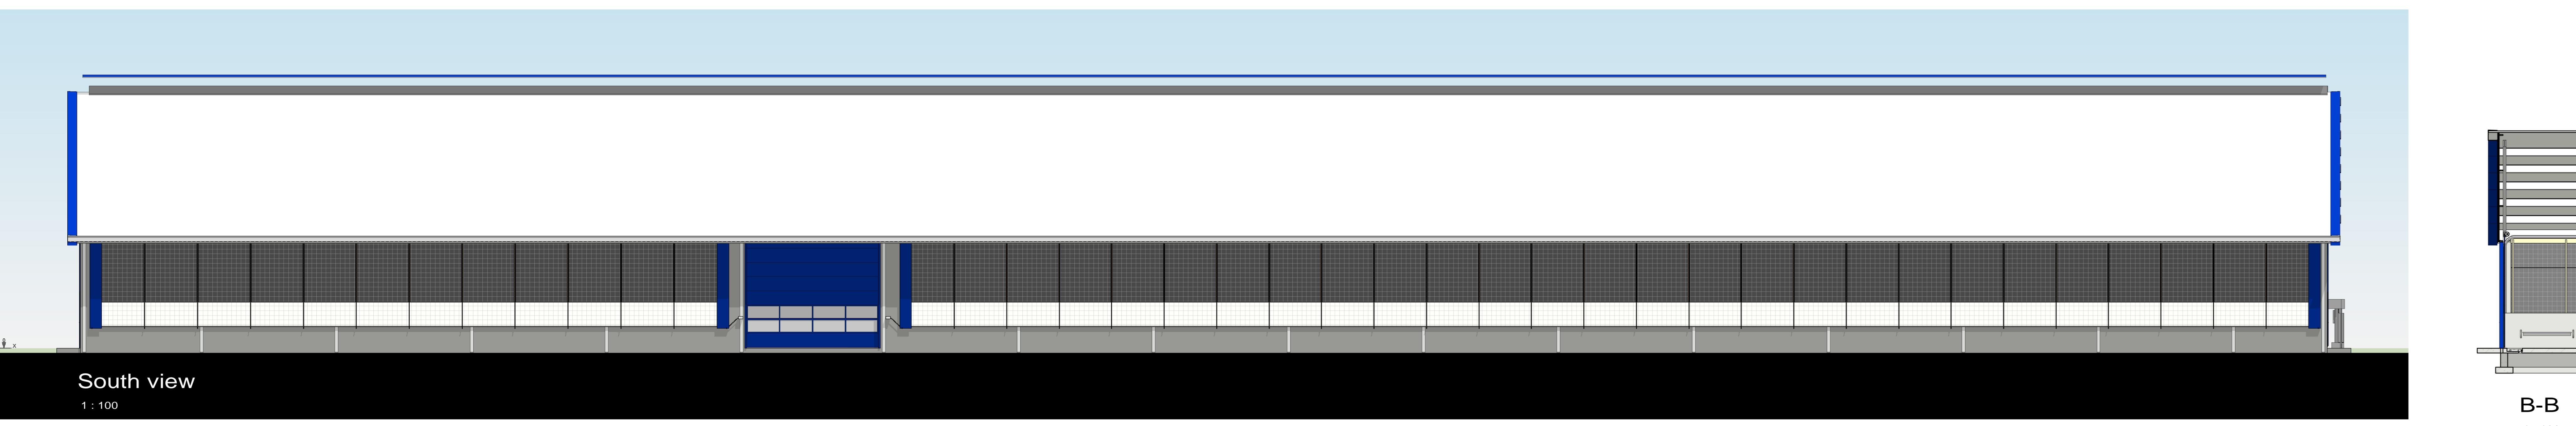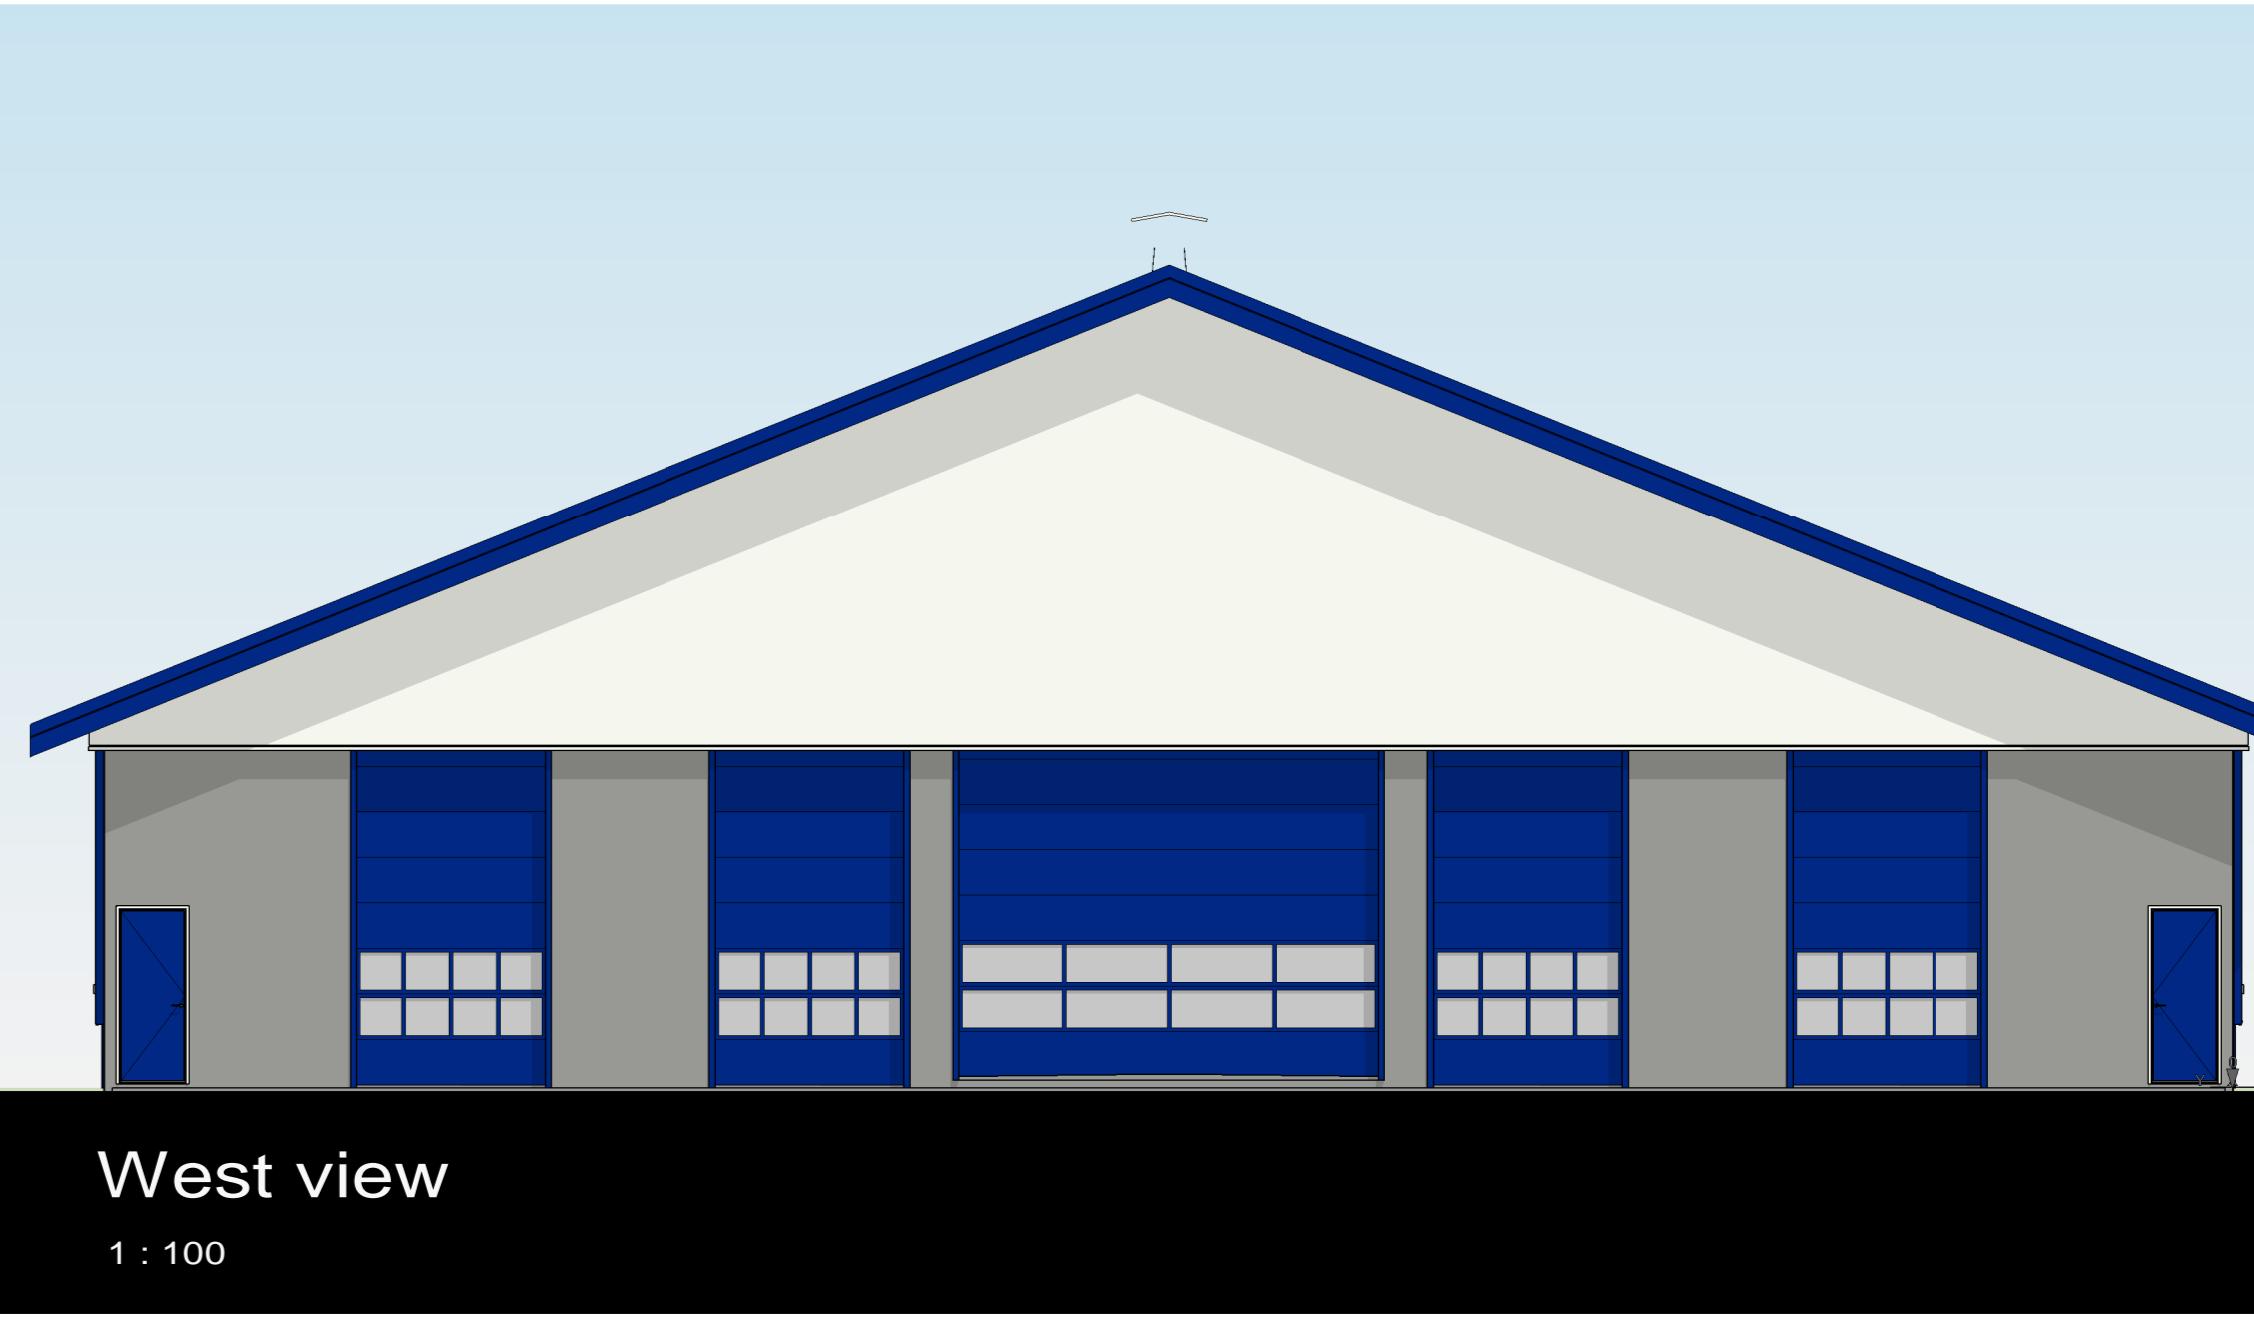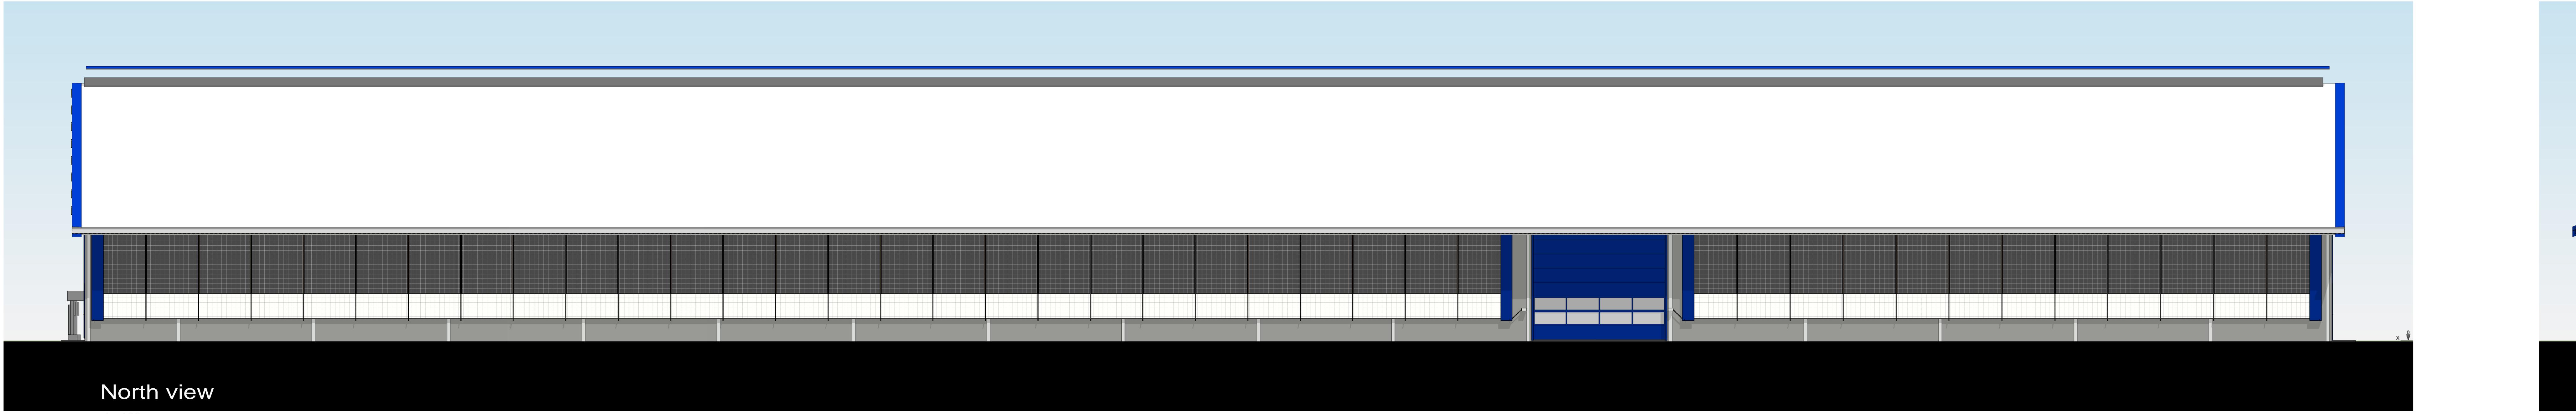









Easy Farming
AGRI PROM
total cow comfort









PROJECT: Tchin Lait Algeria
ONDERWERP: 20 en 21 floor plan, facade view, sections en 3D
BLADNUMMER: B.4.01

PROJECT: Algeria
ONDERWERP: 20 en 21 floor plan, facade view, sections en 3D
BLADNUMMER: B.4.01

TEKENAAR: Geert
DATUM: 05-08-2019
GEWOOGD:
B
C
D
FORMAT: A0

OPDRACHTGEVER: Agrifrom
Nieuwleusen

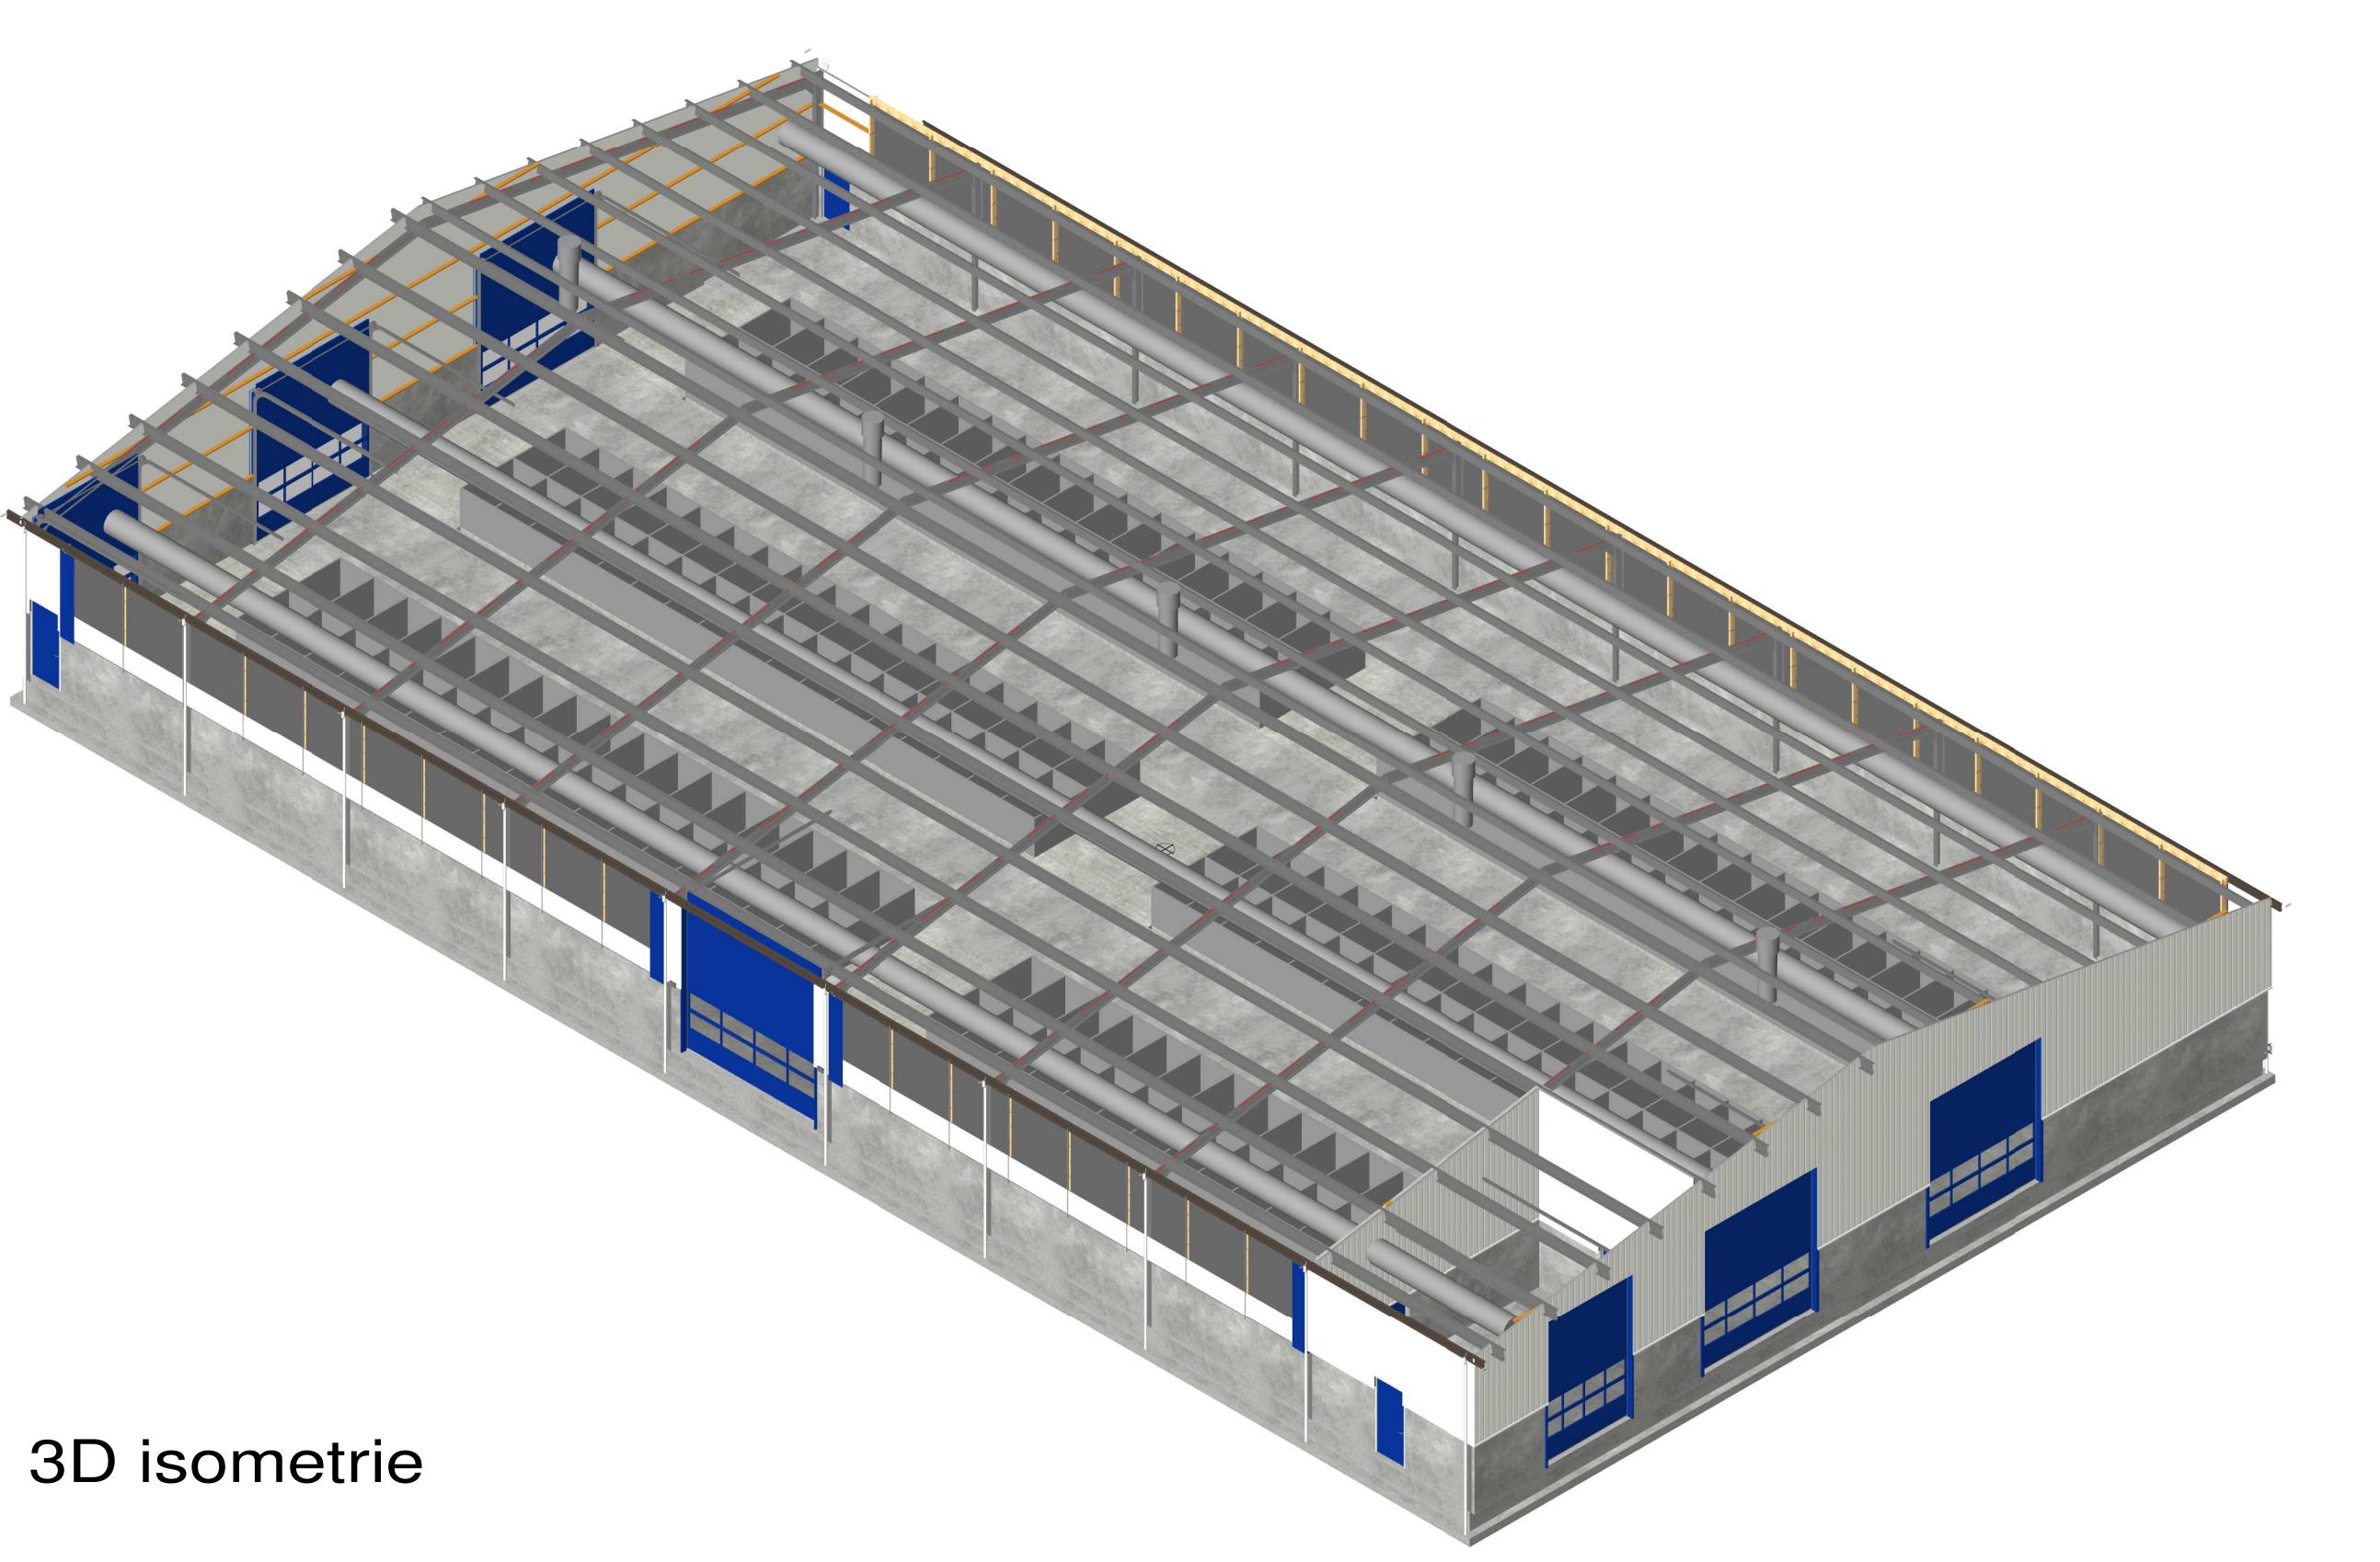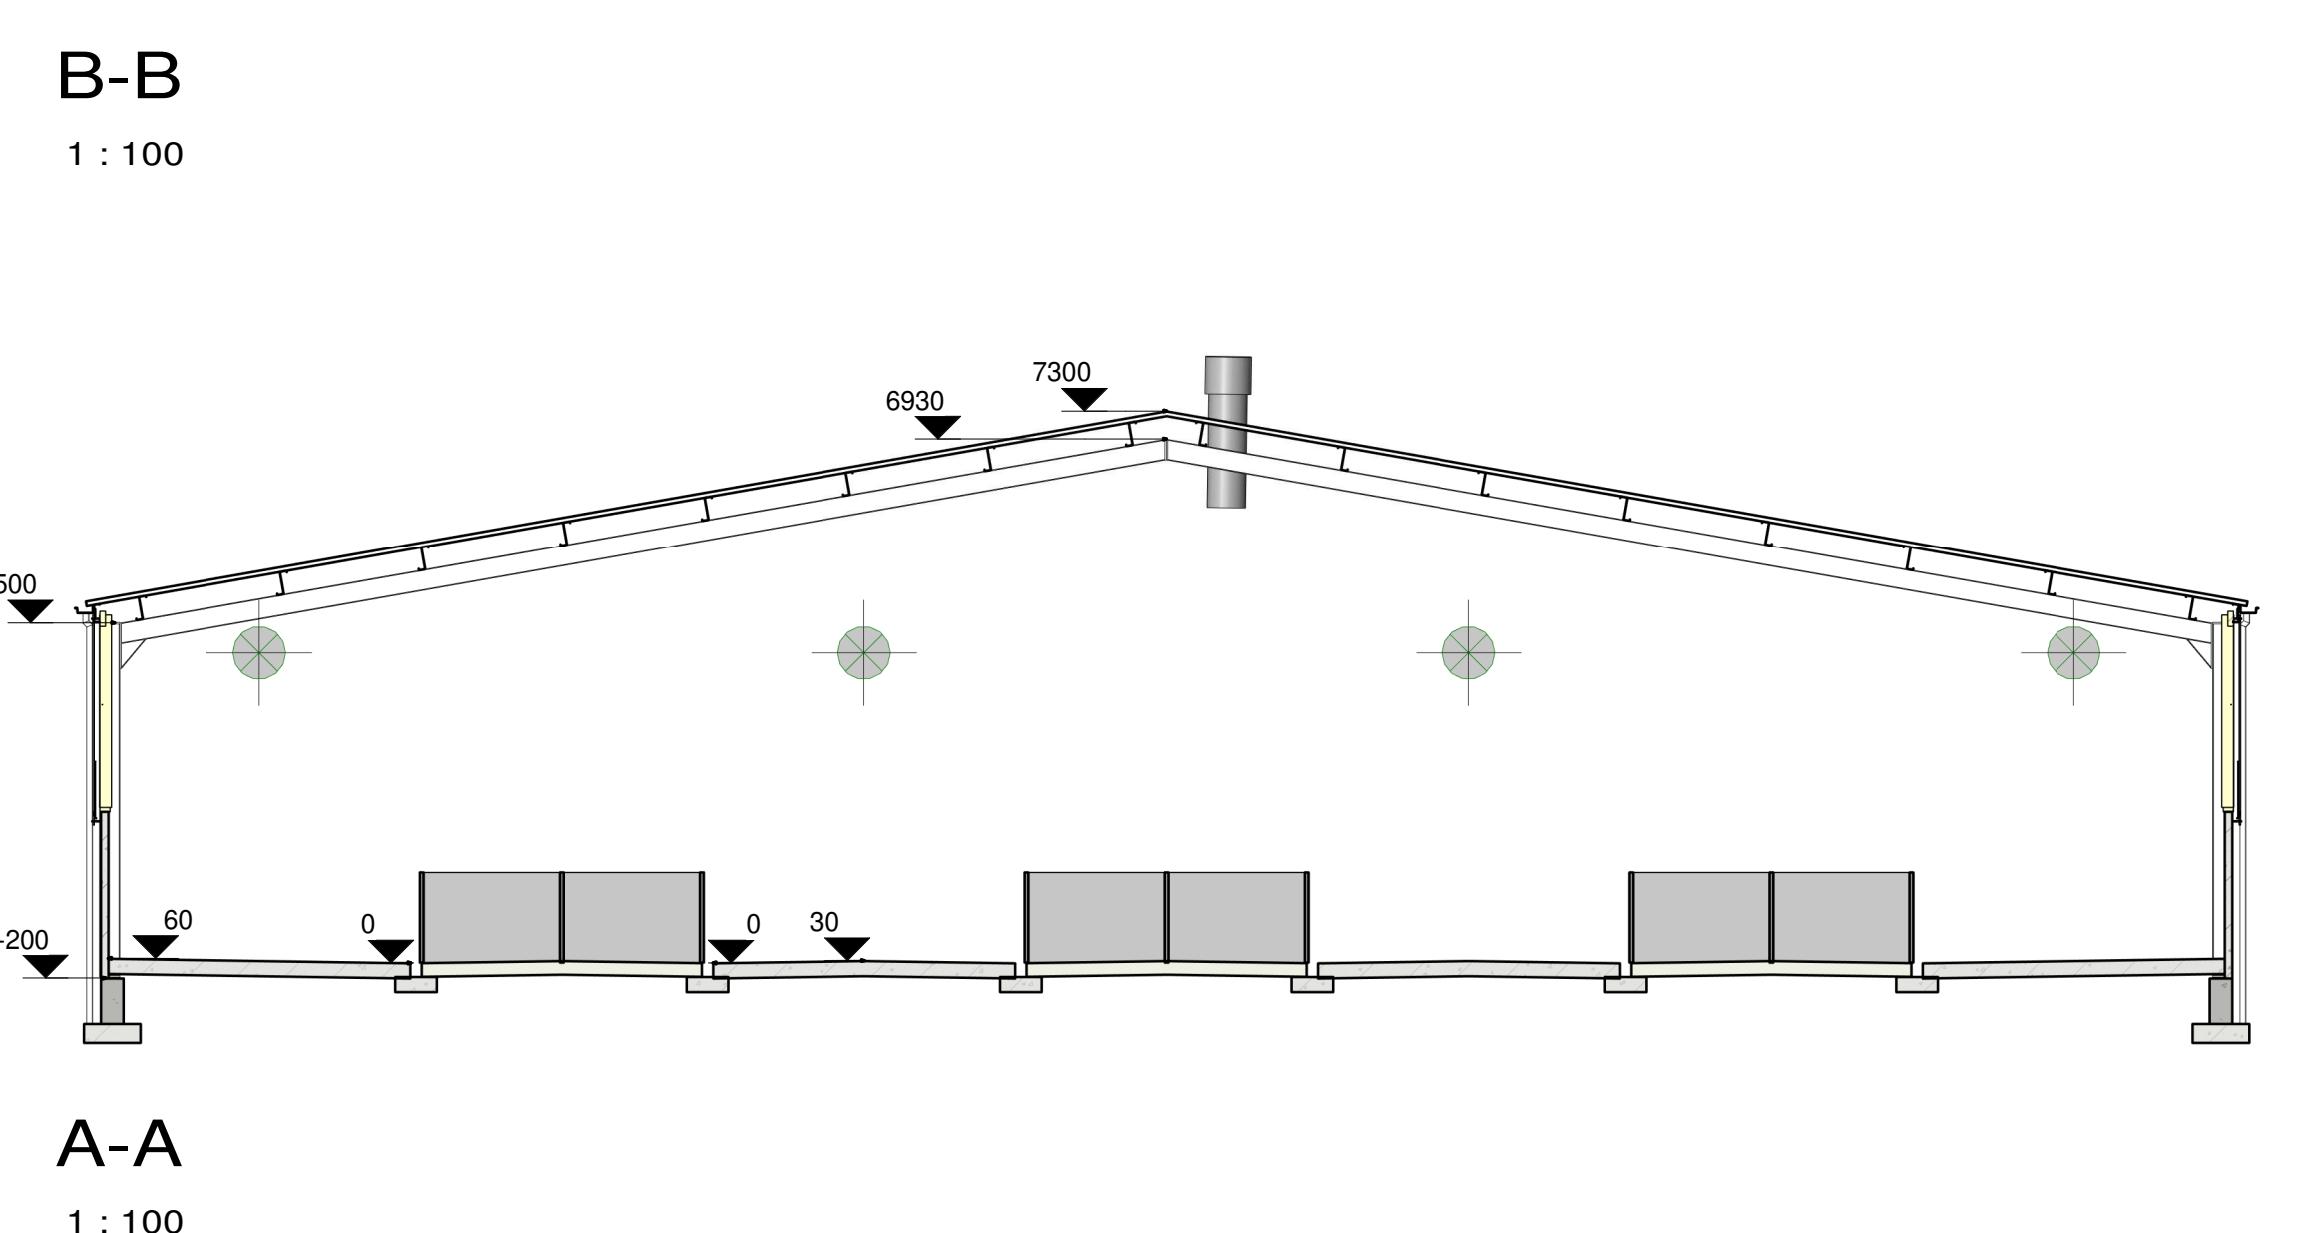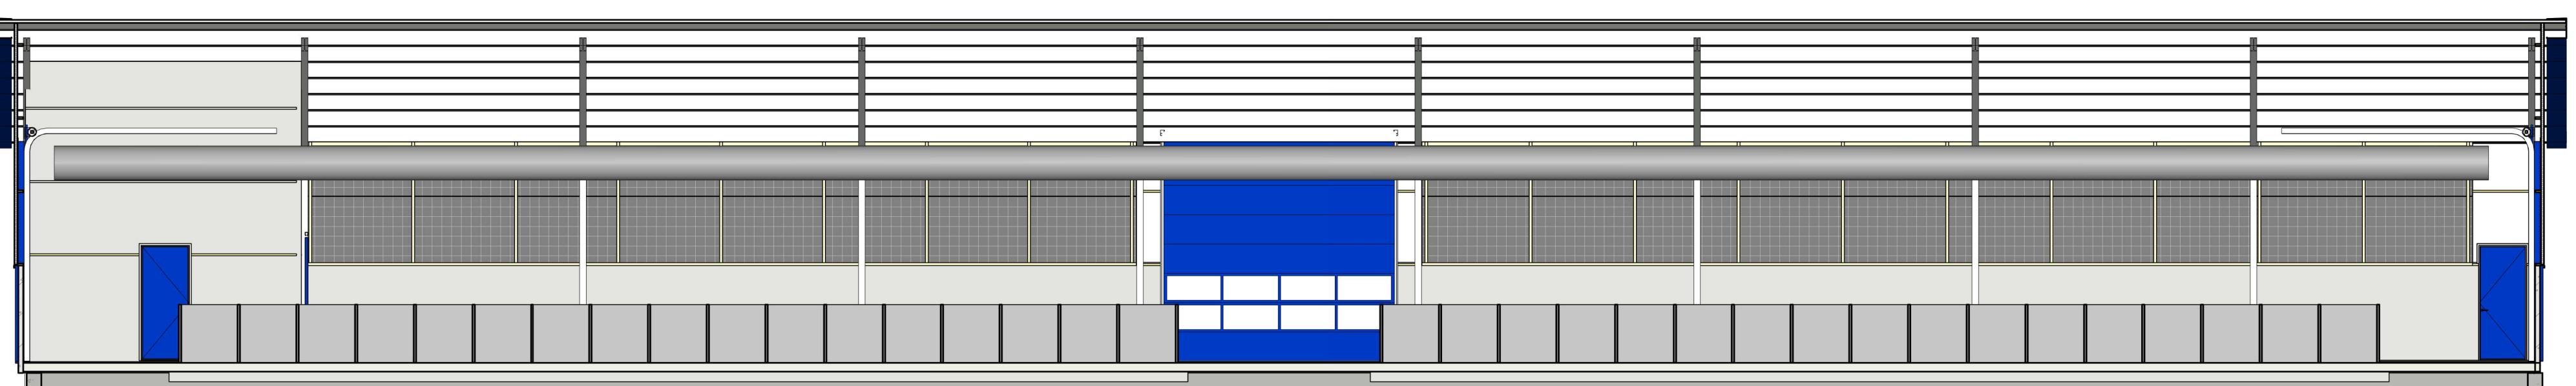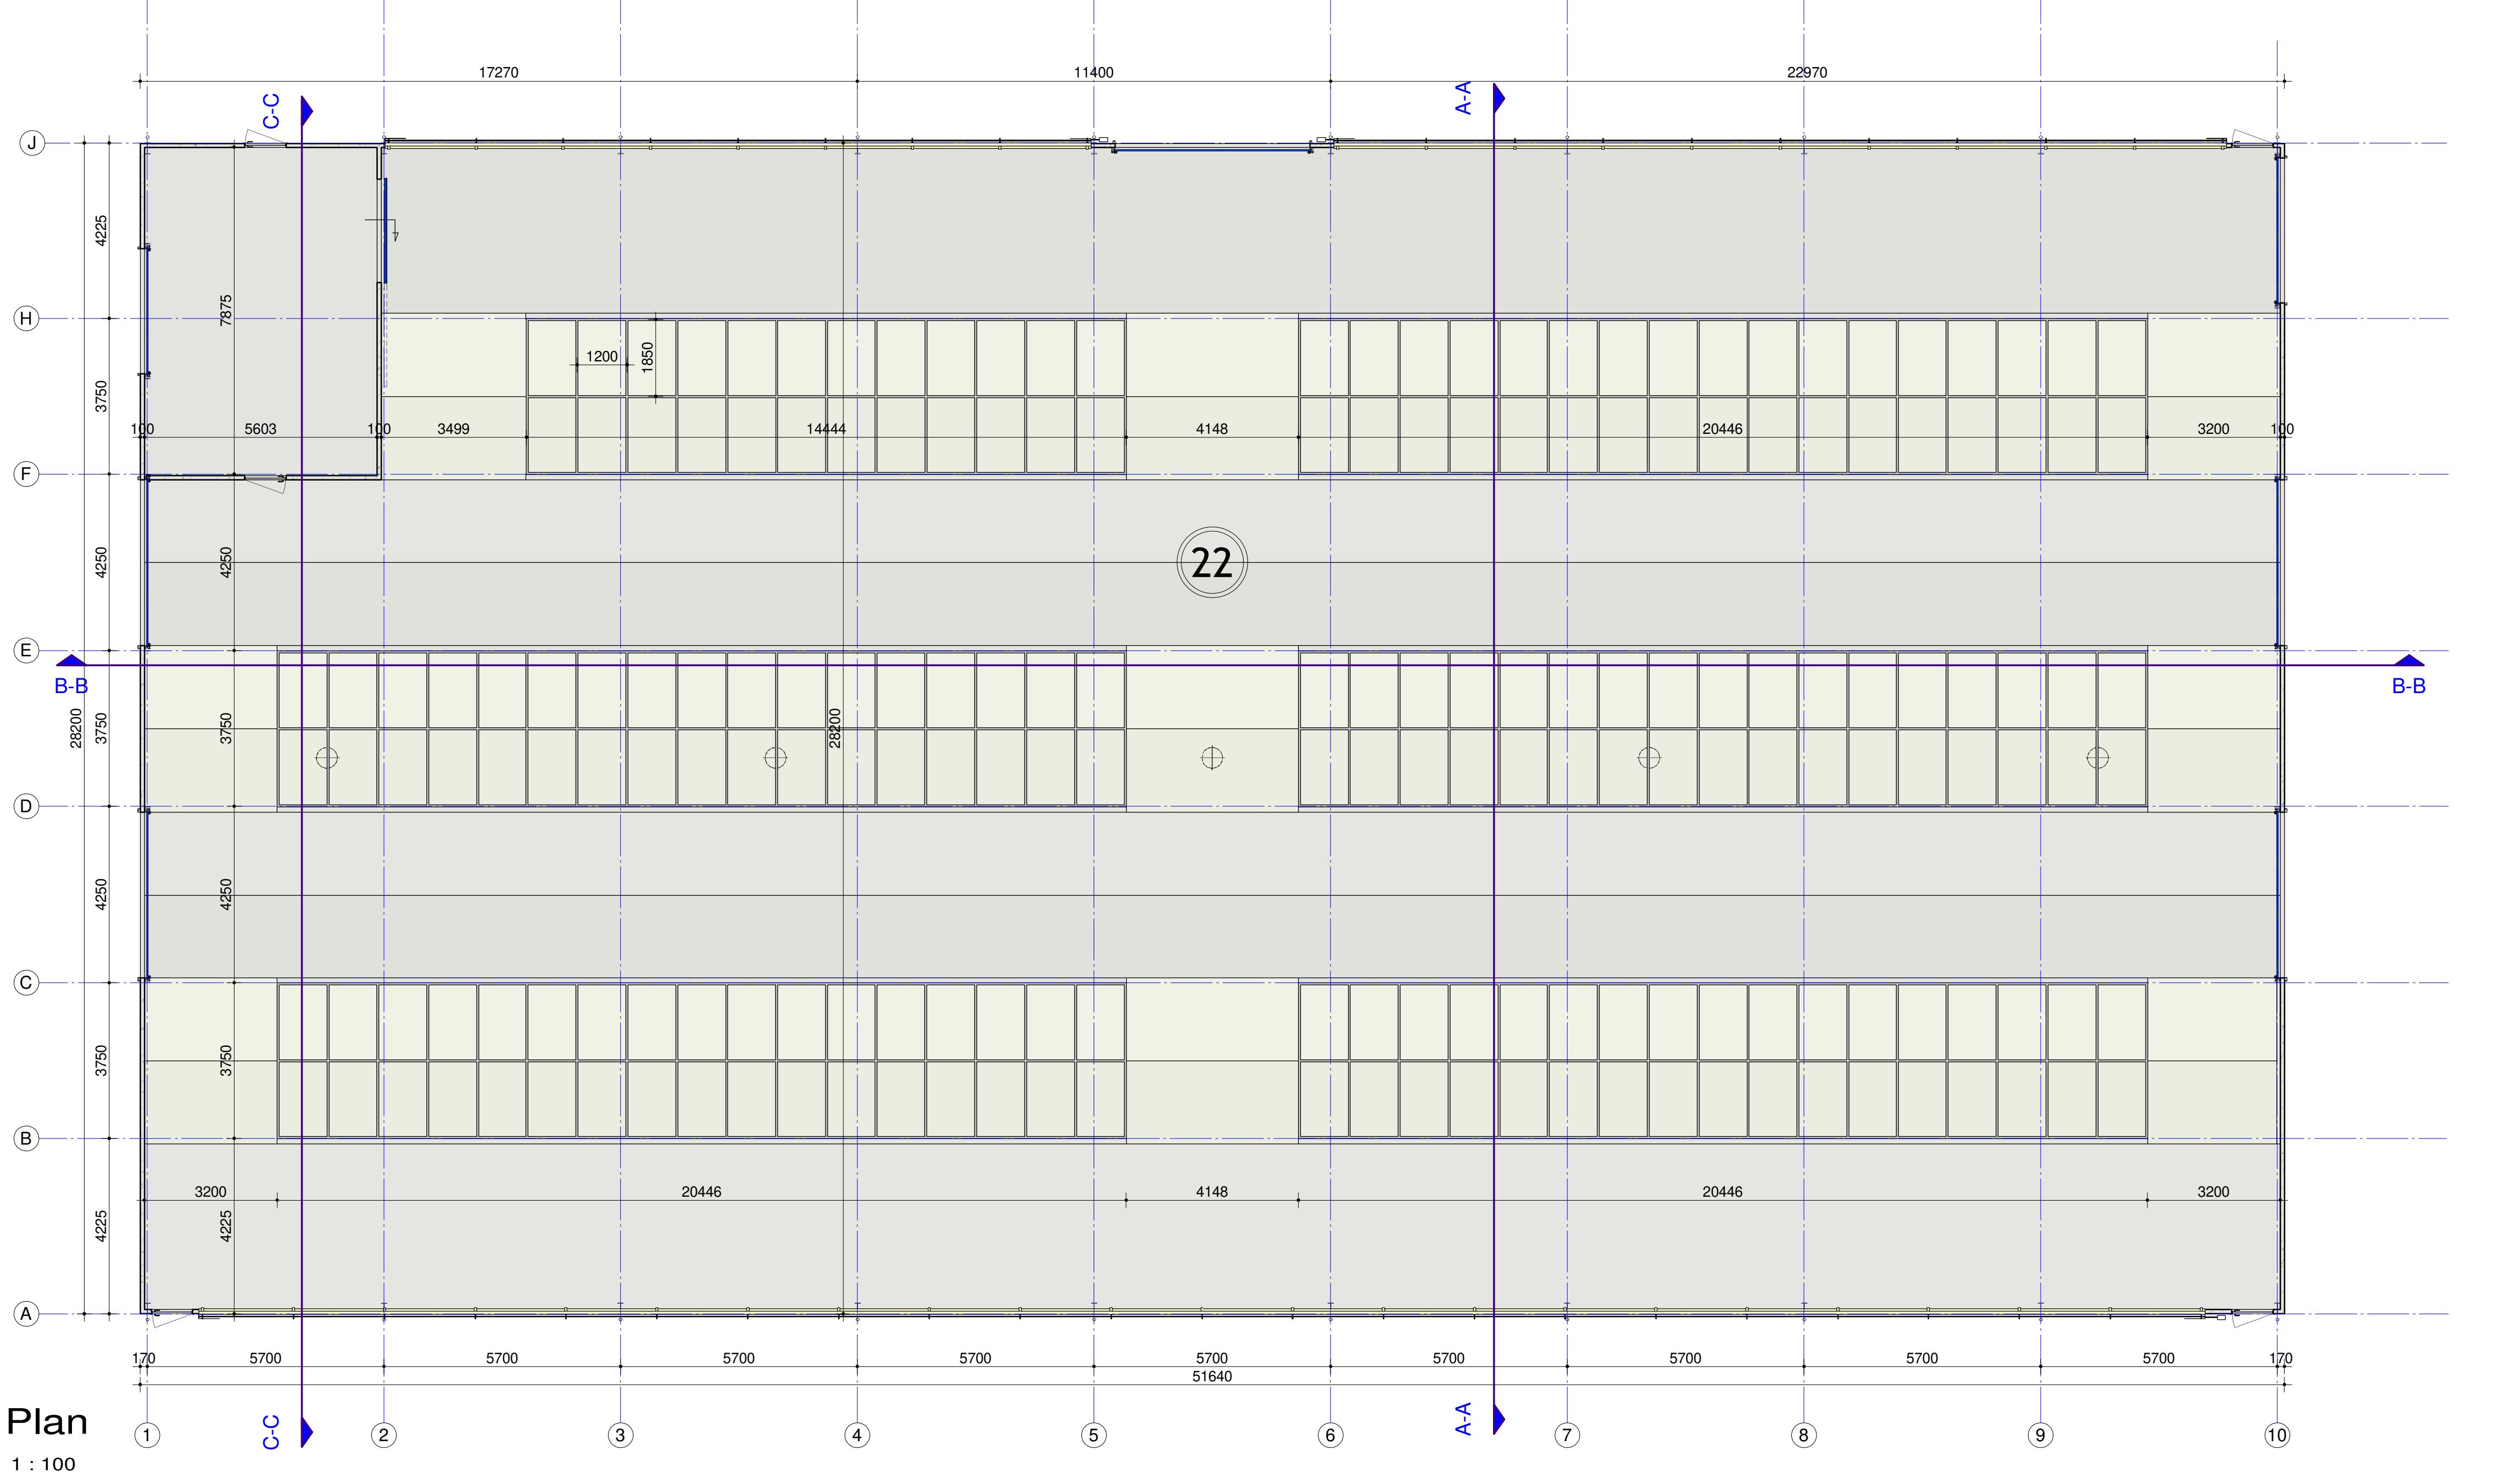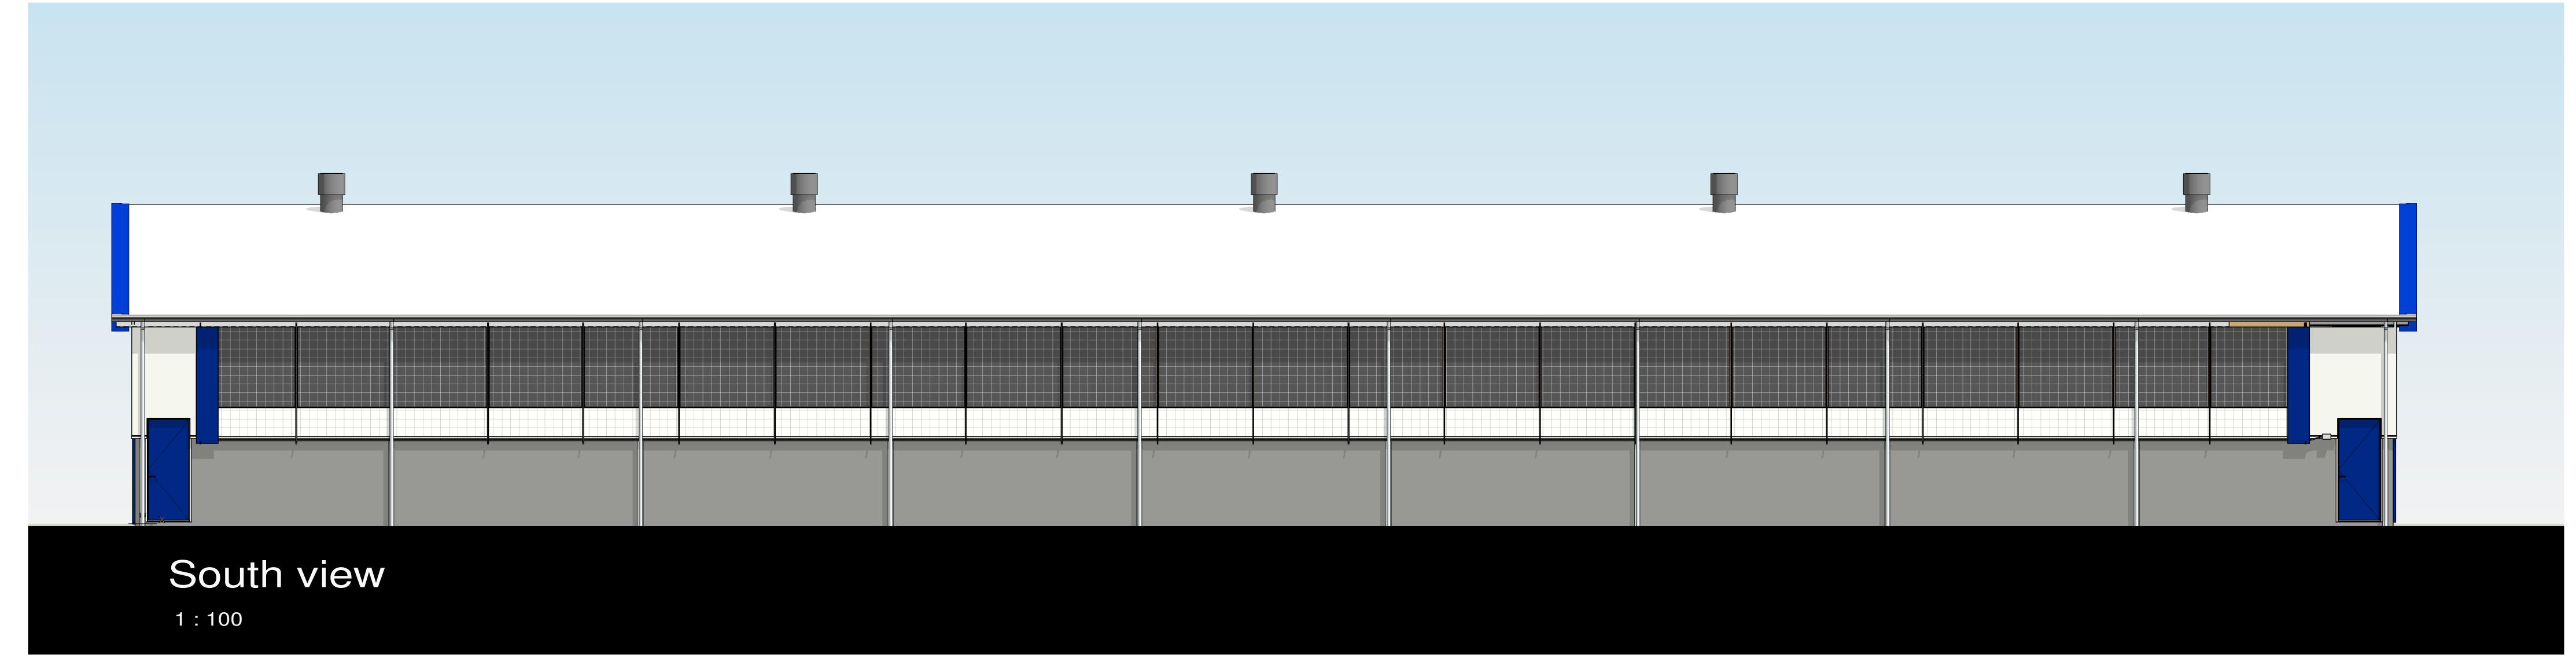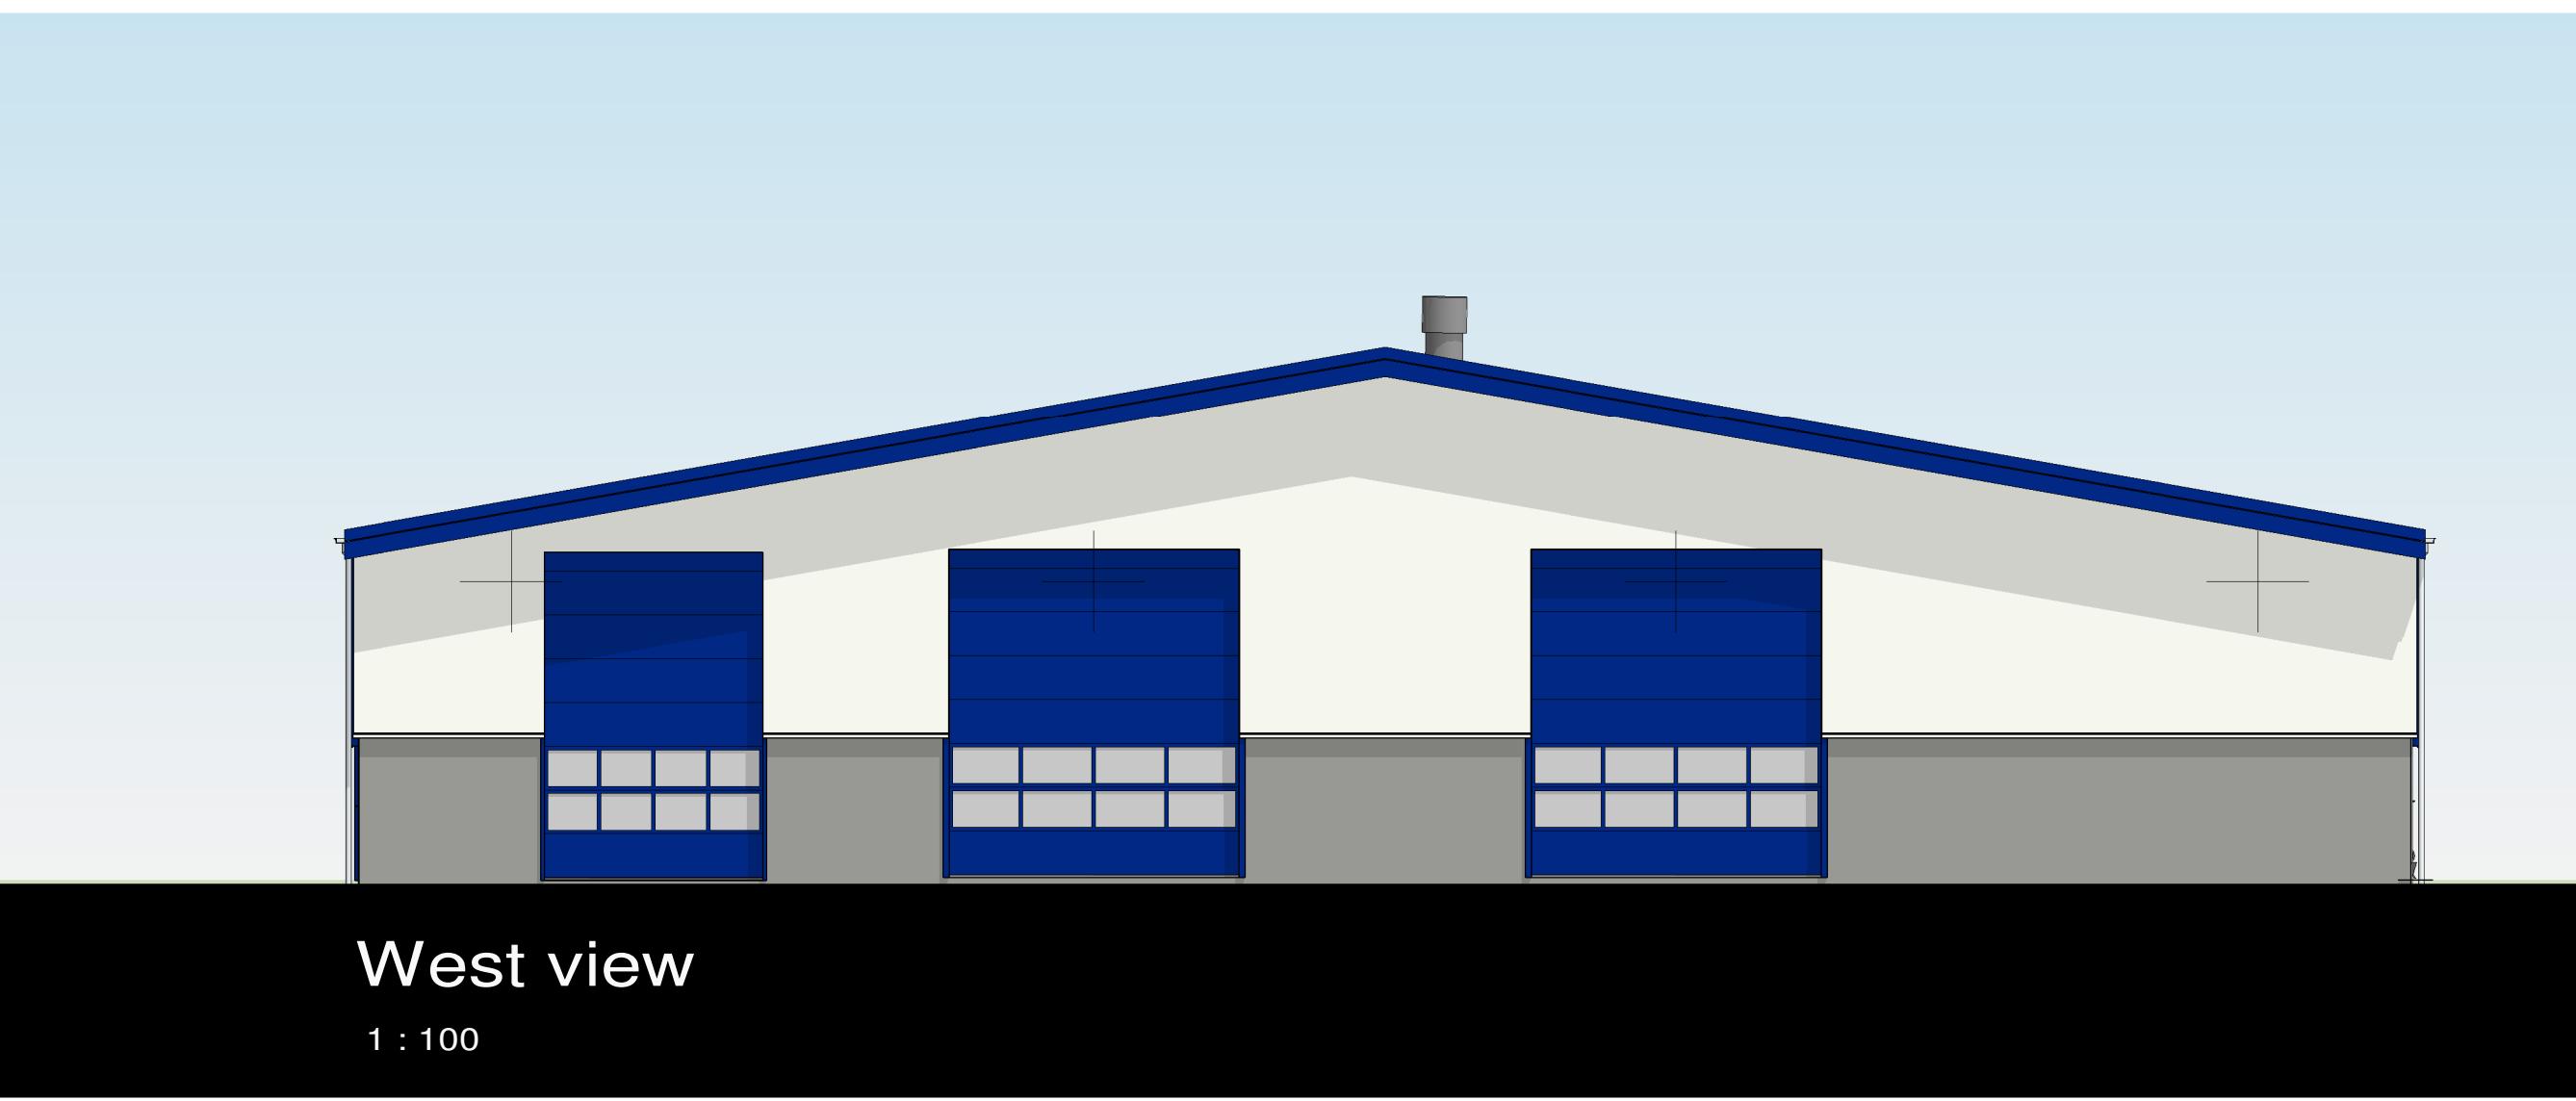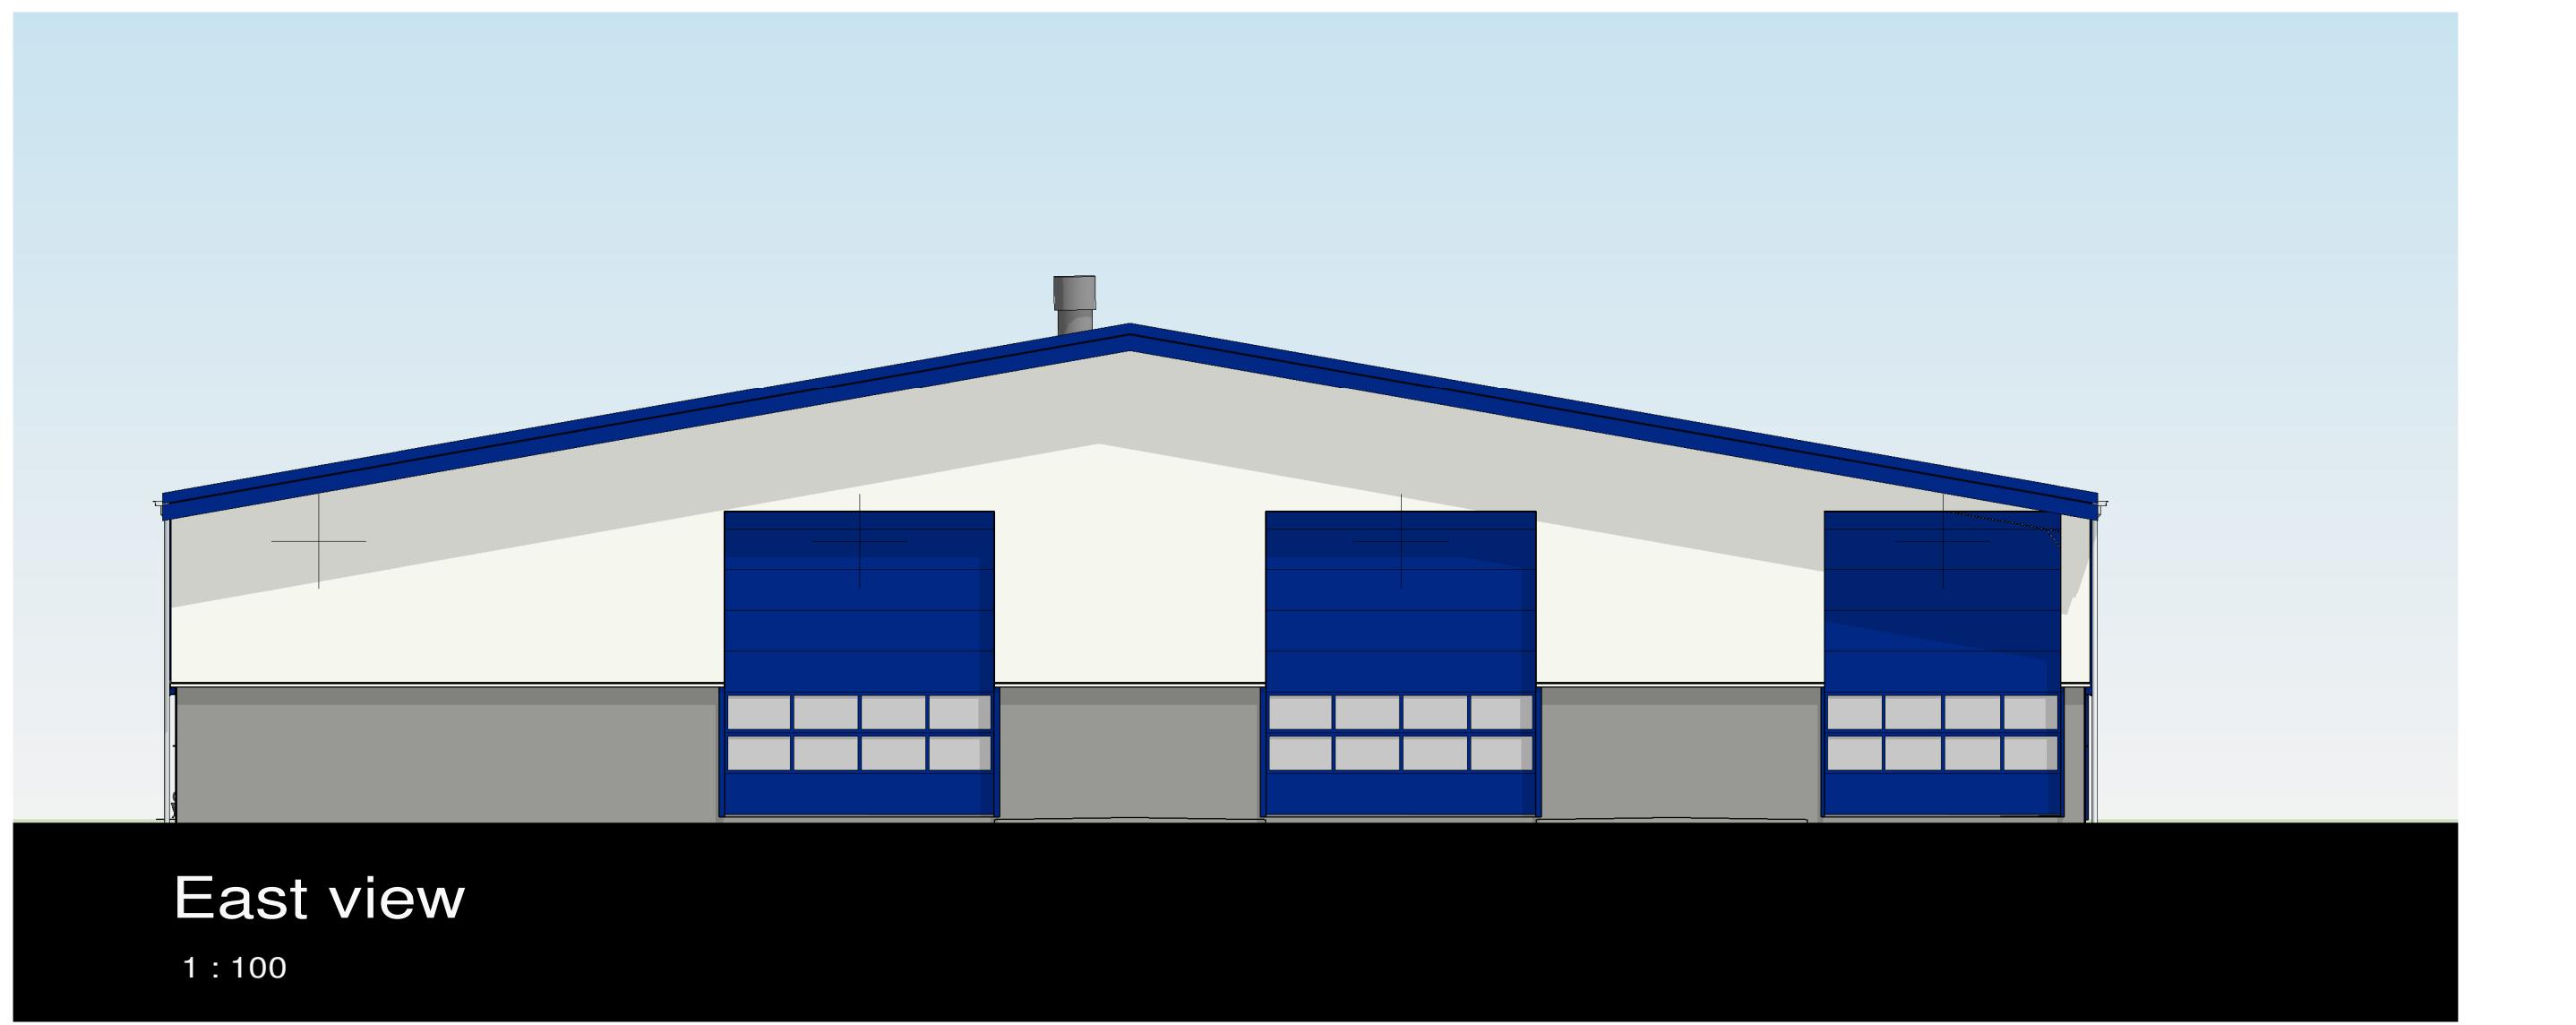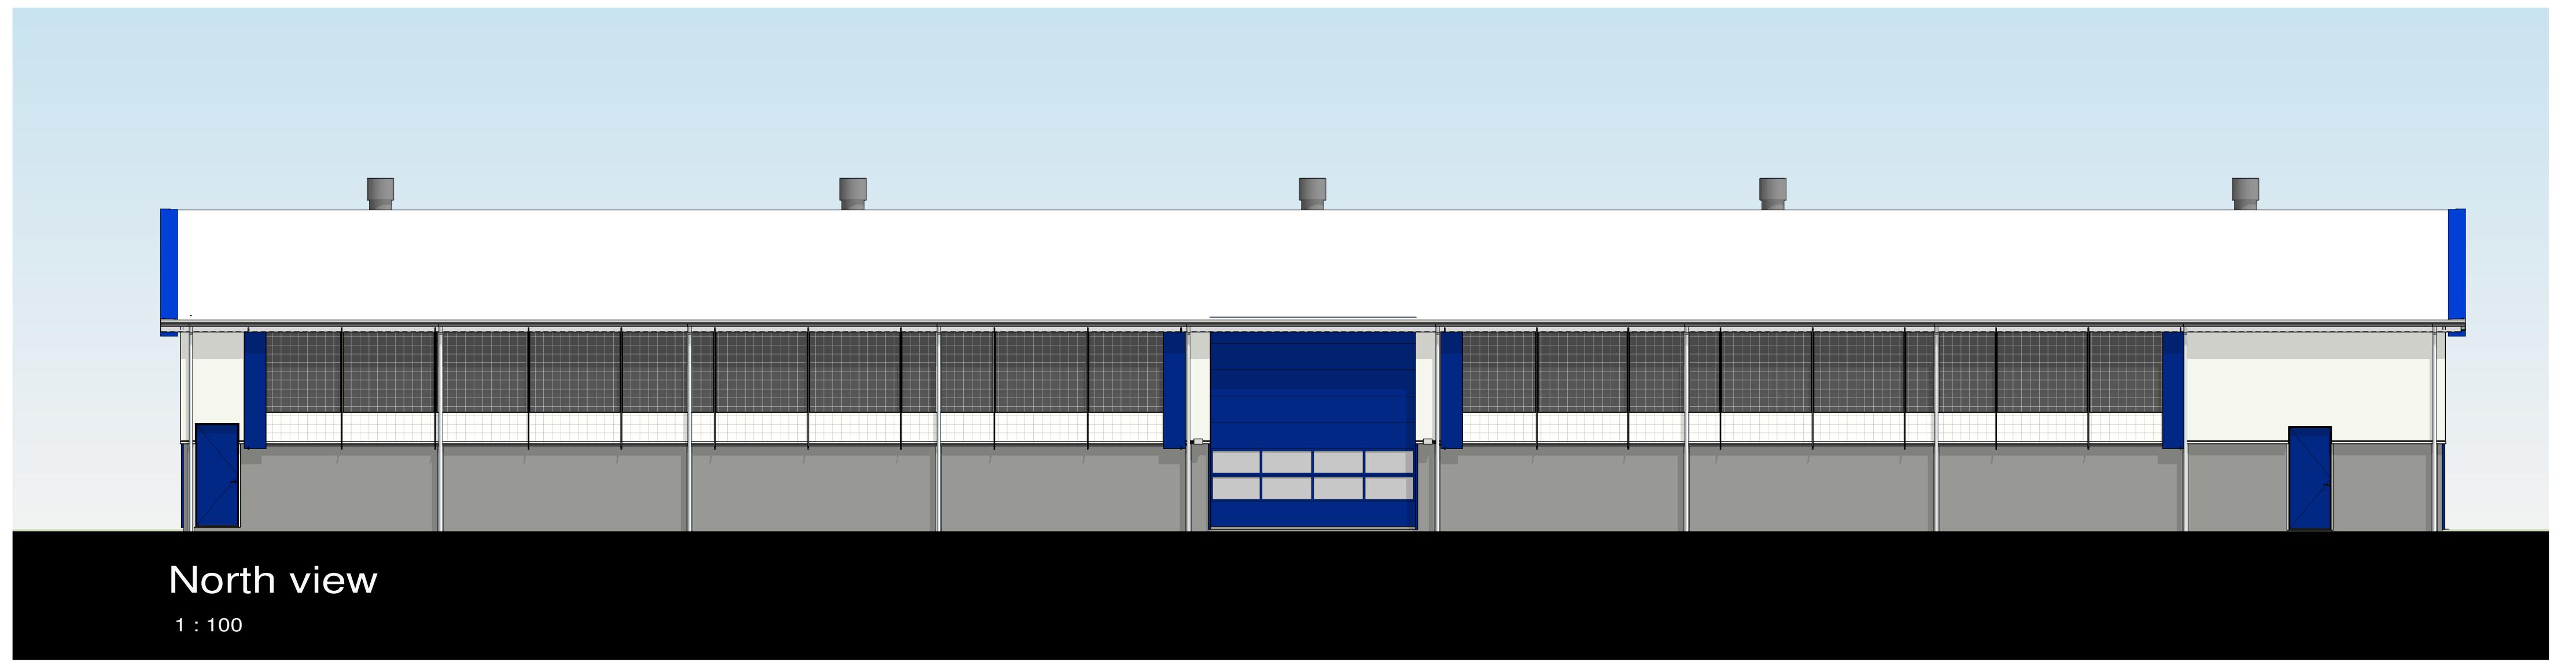

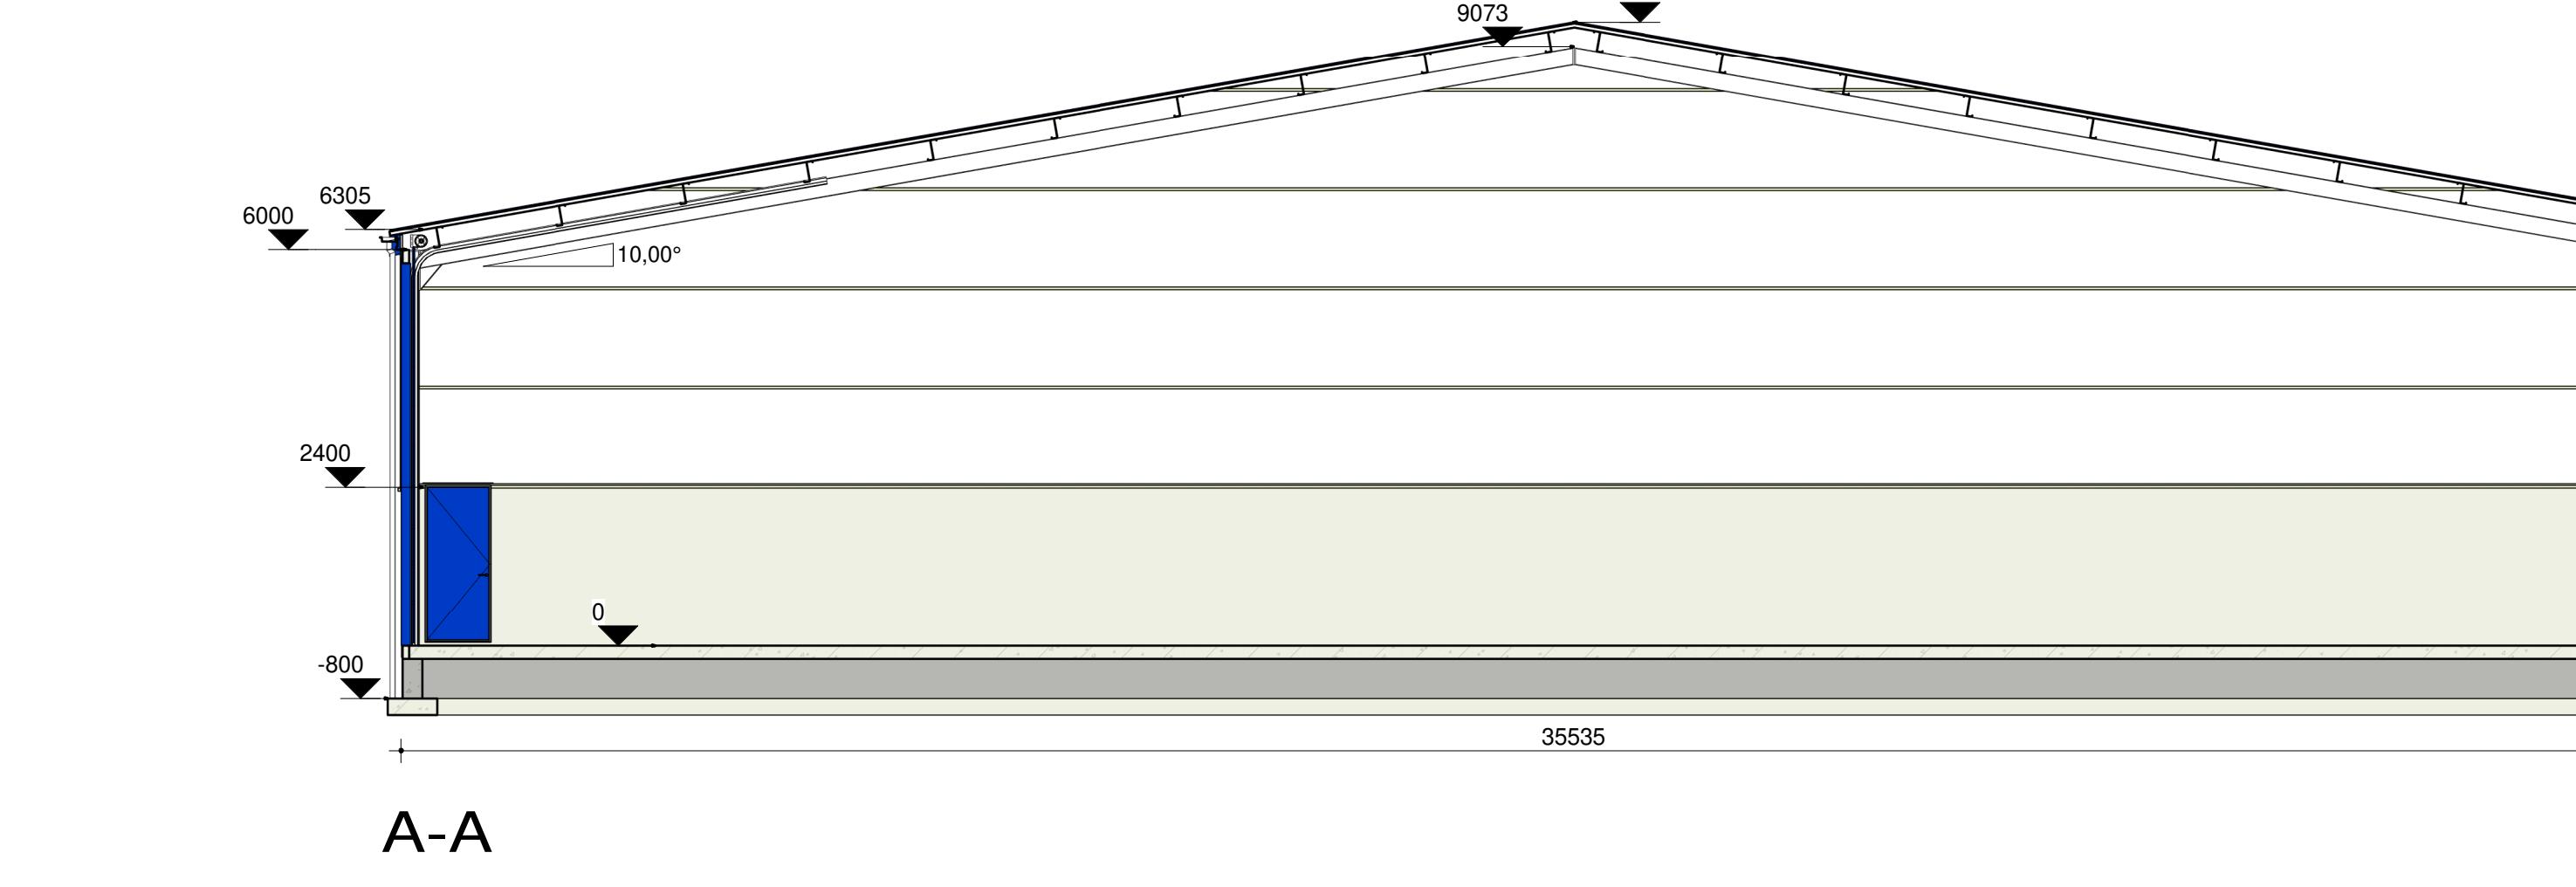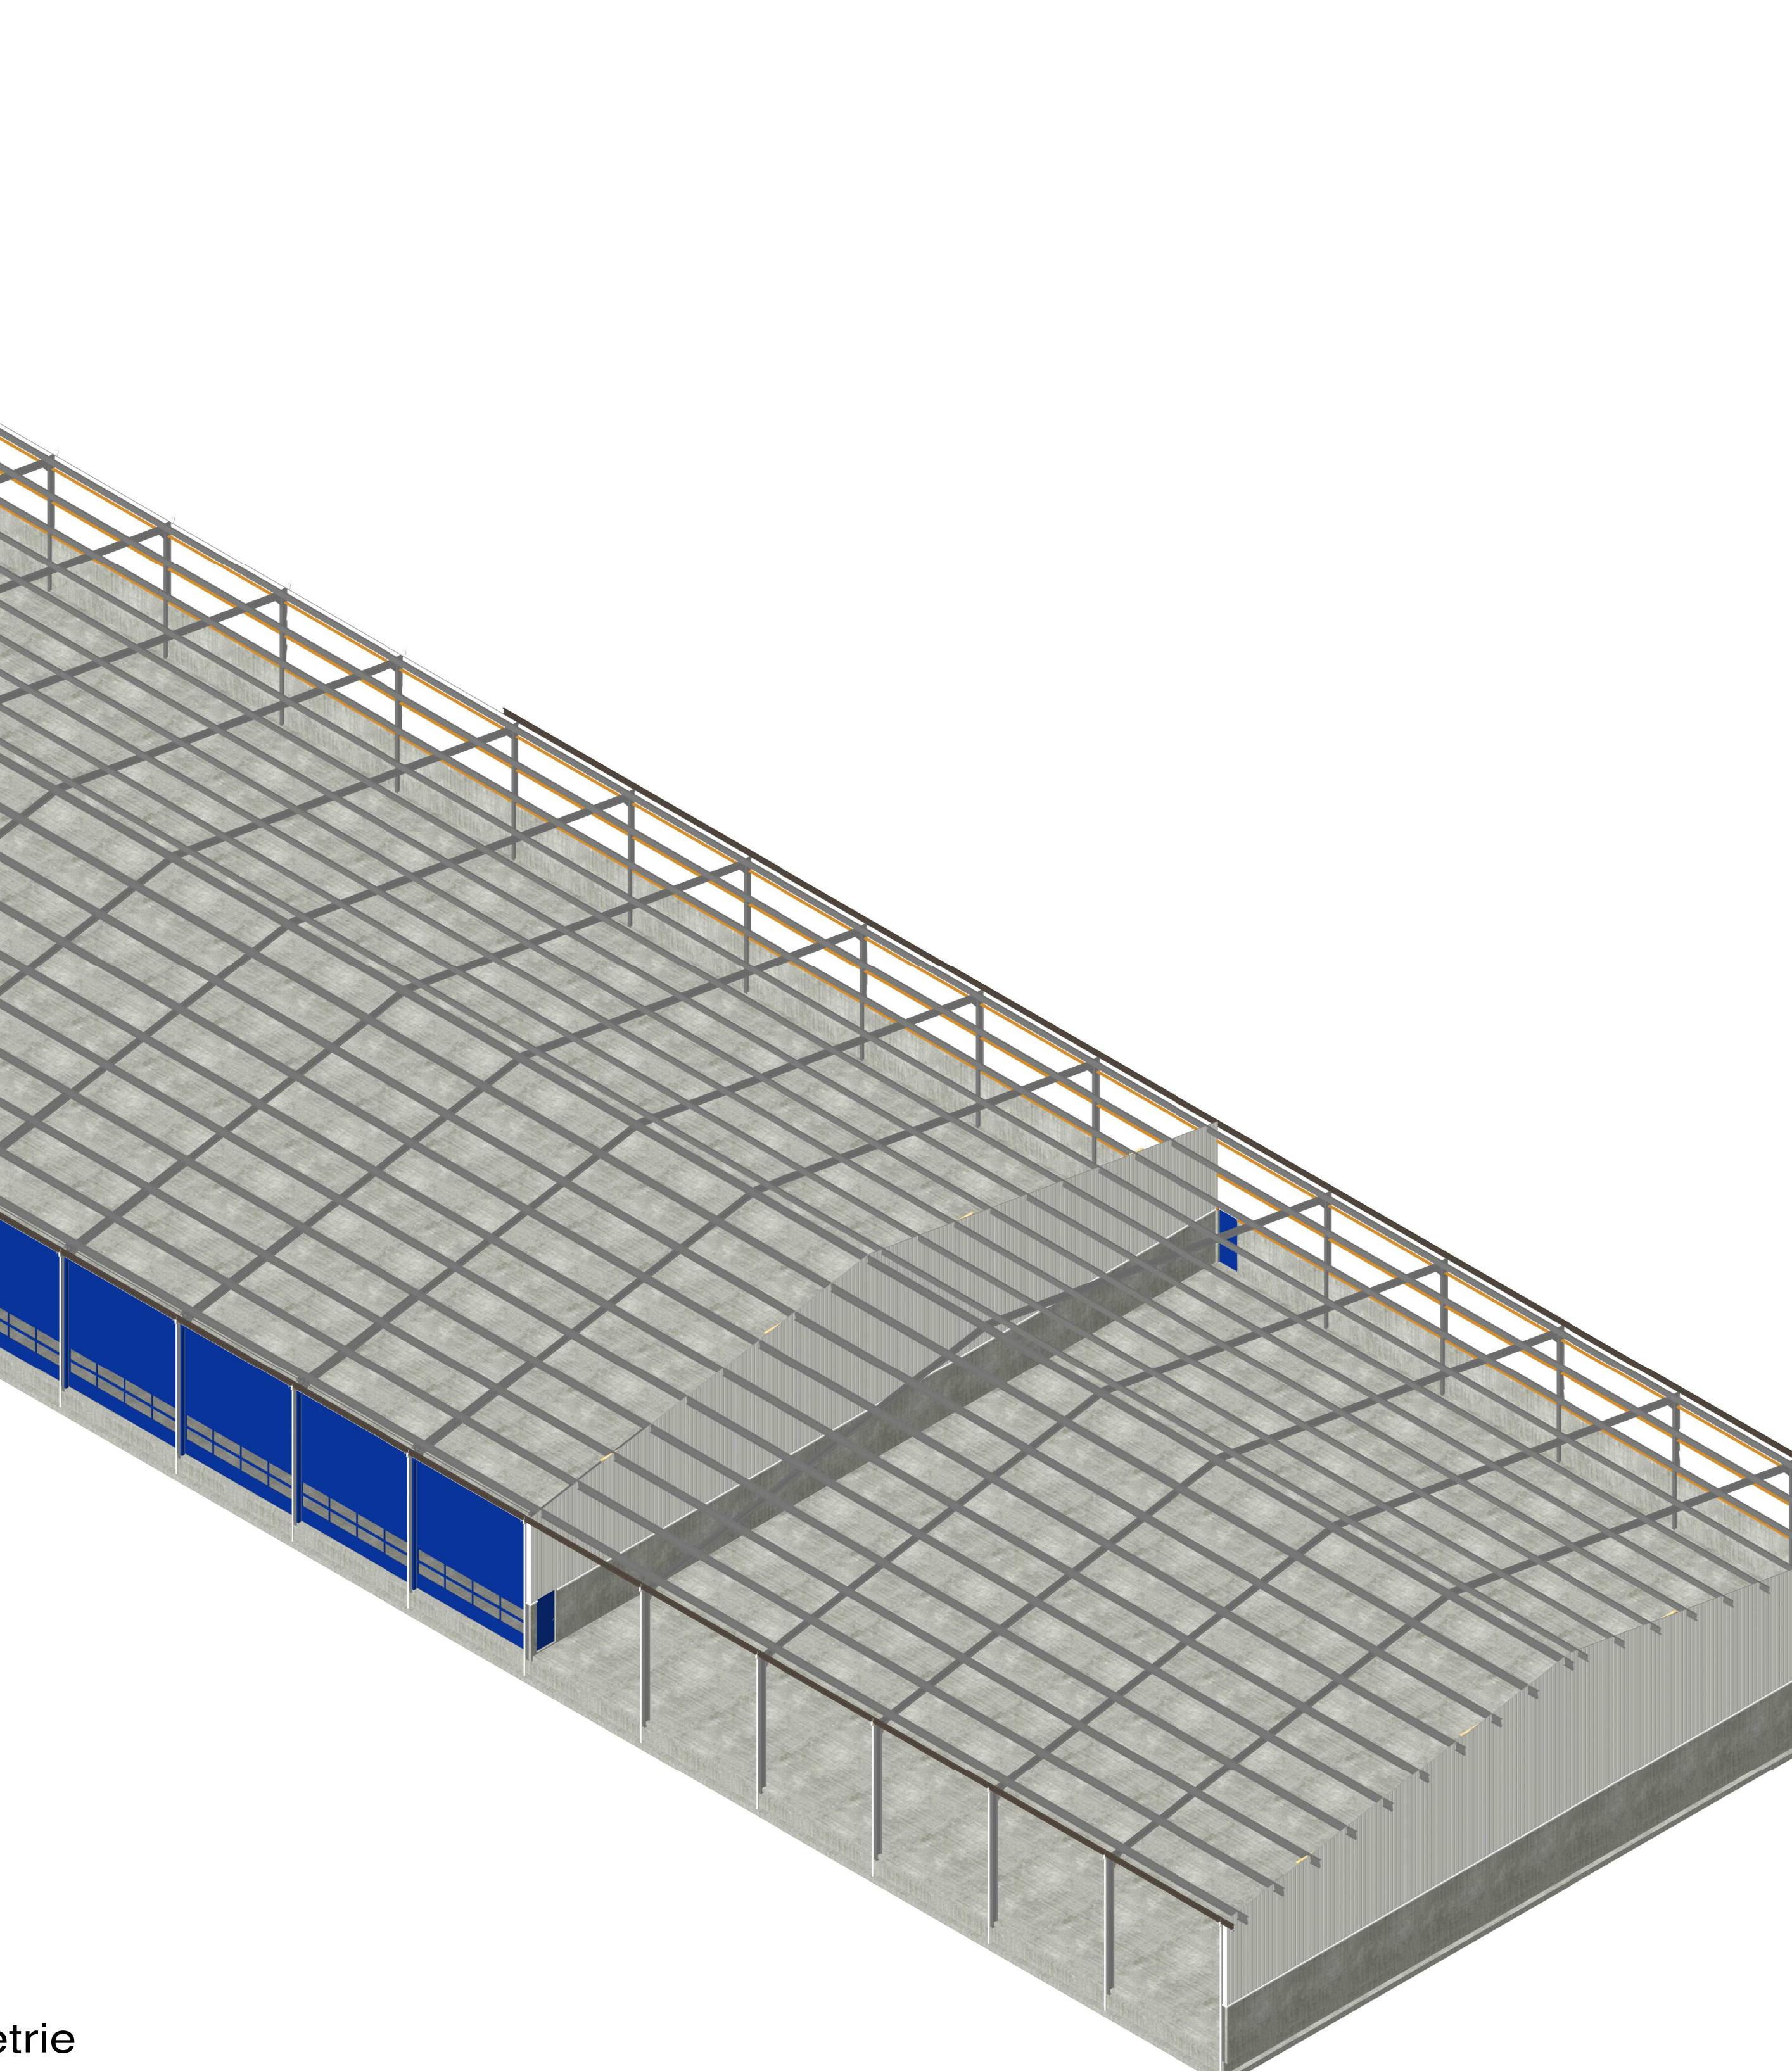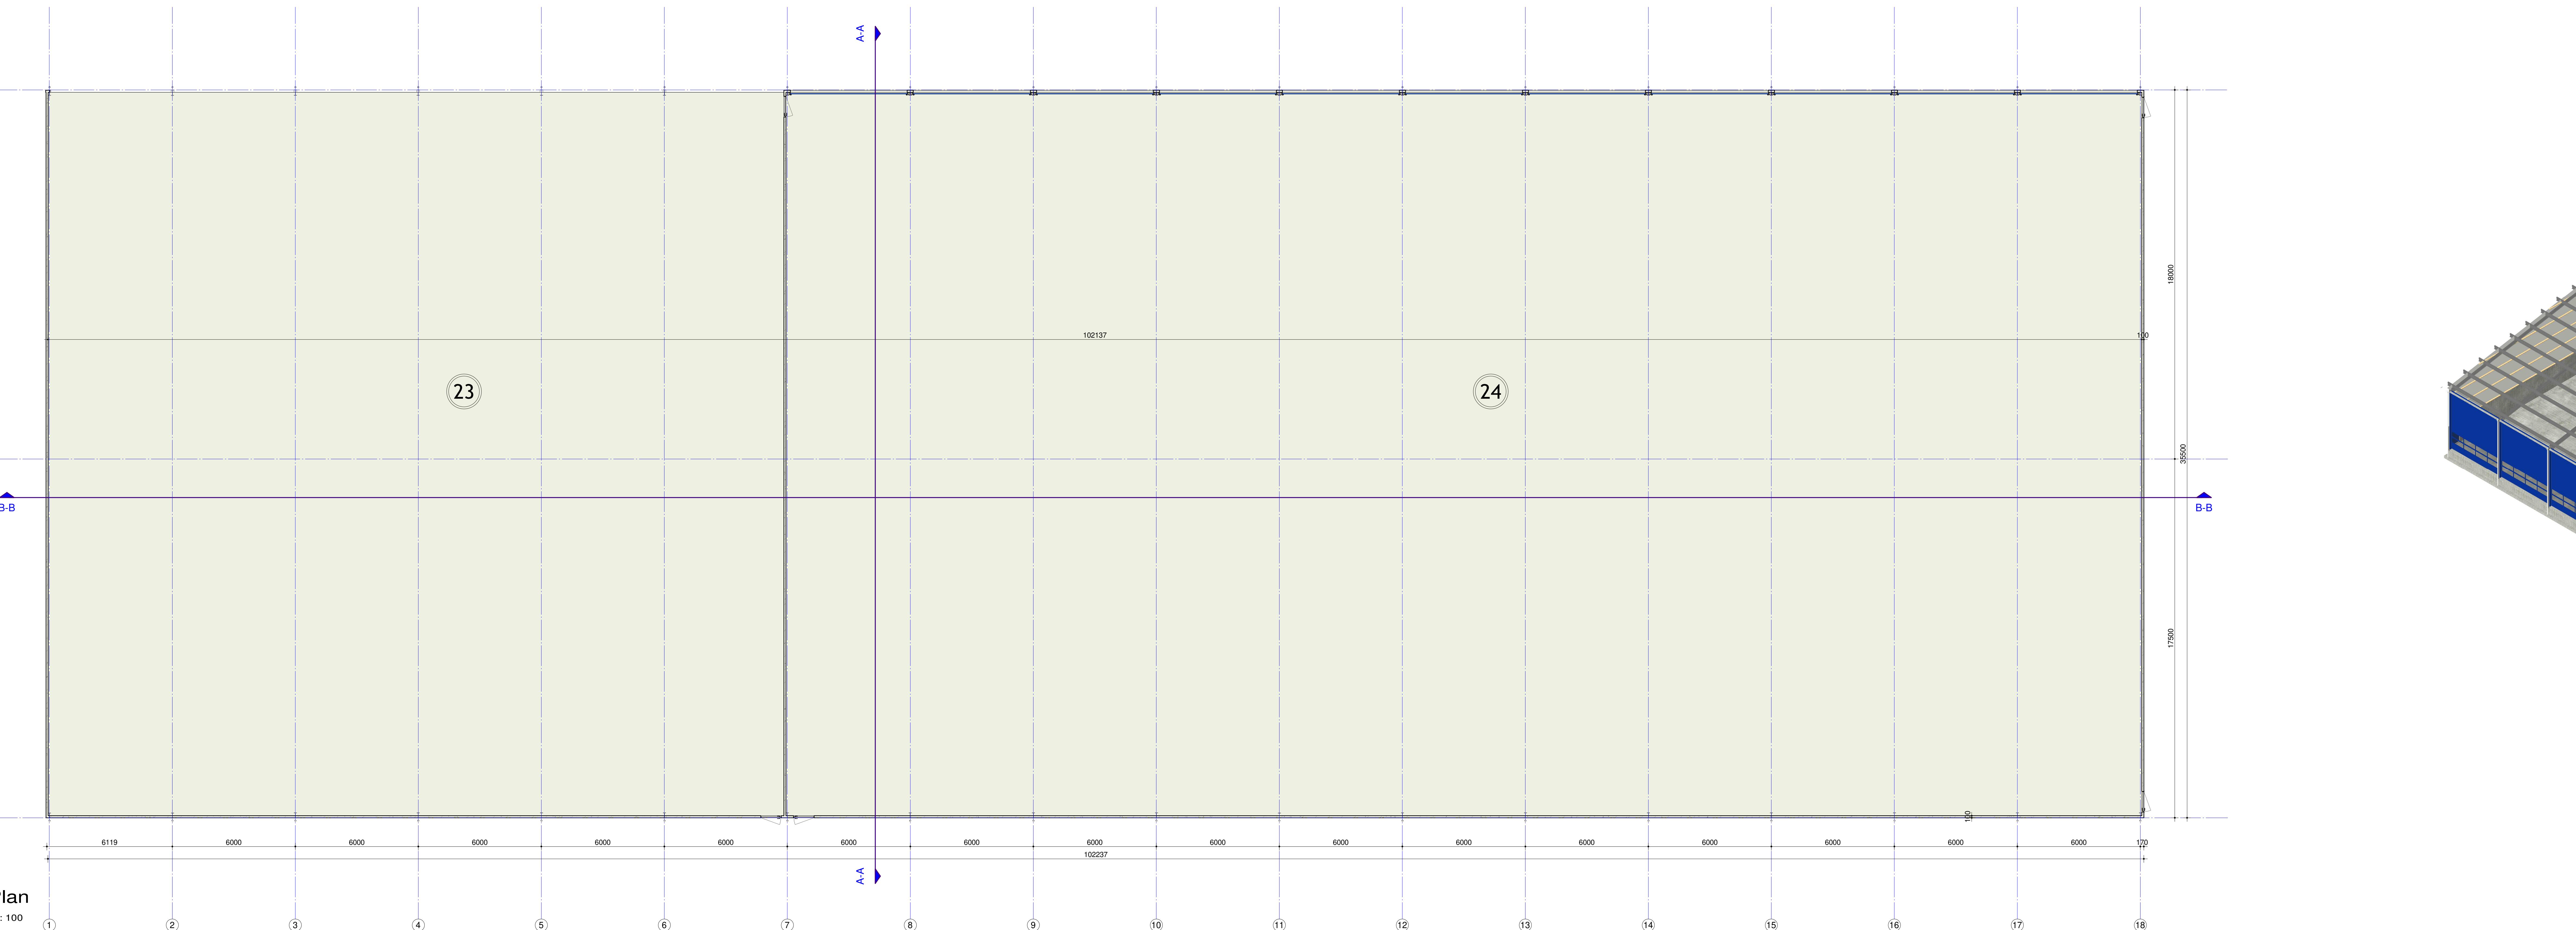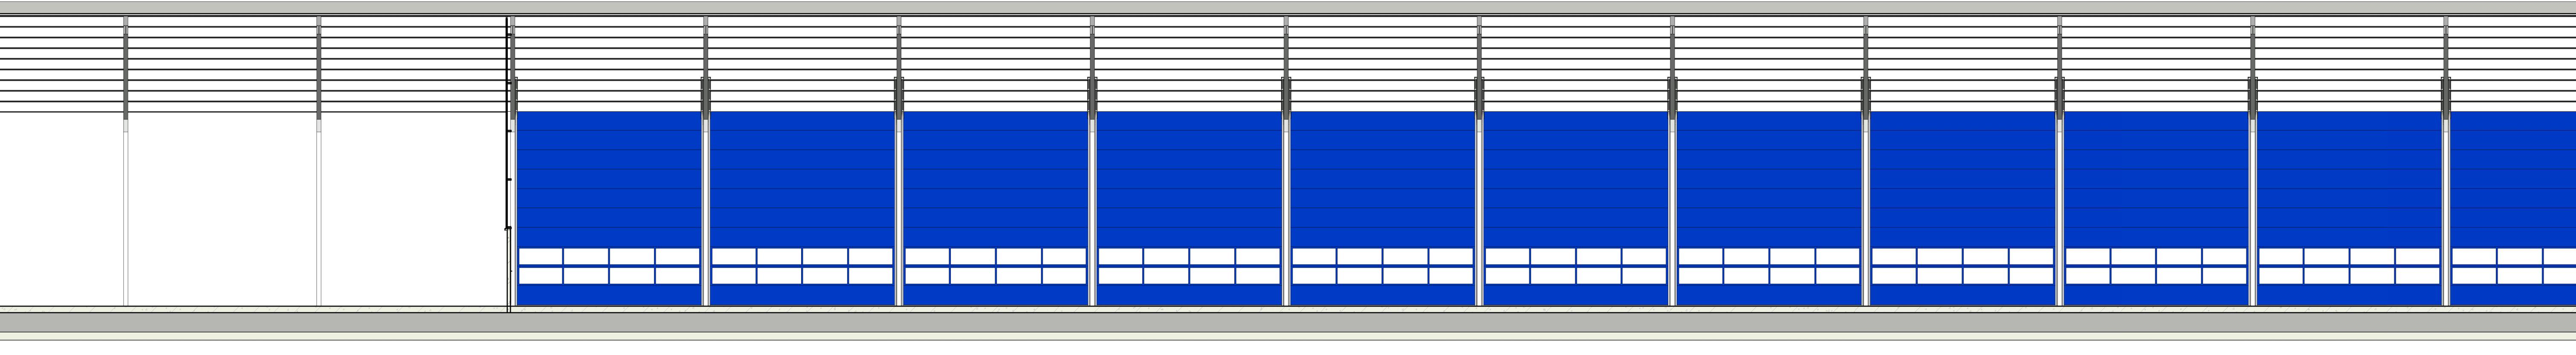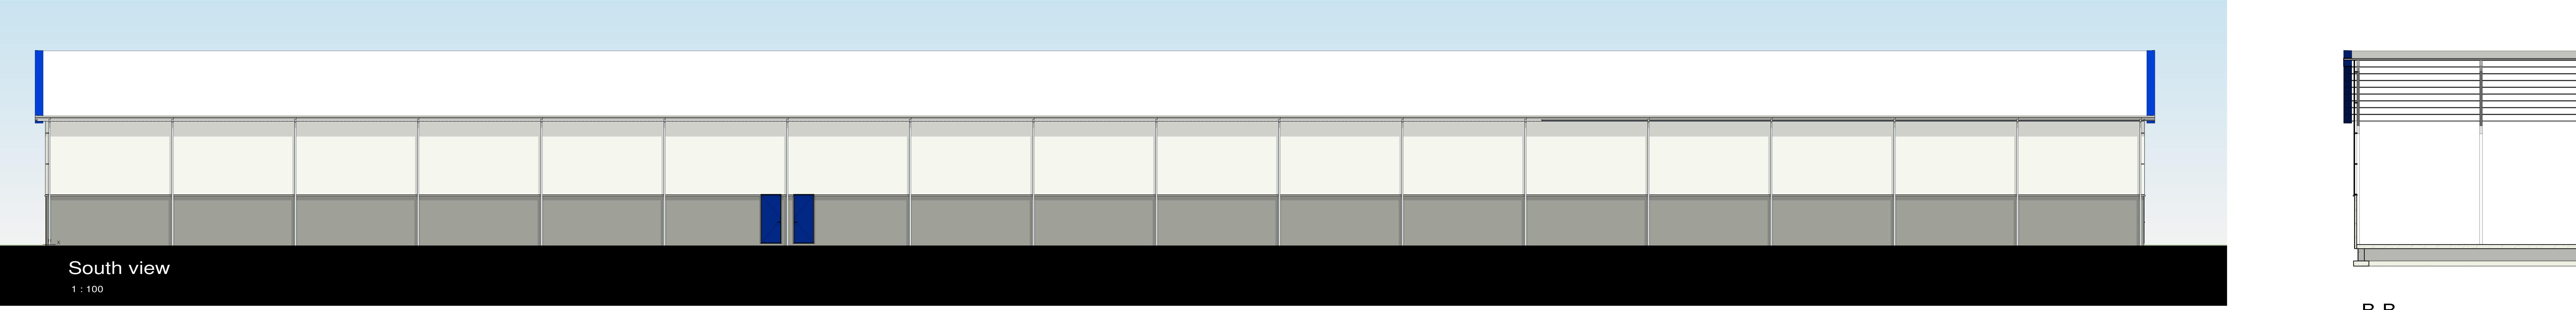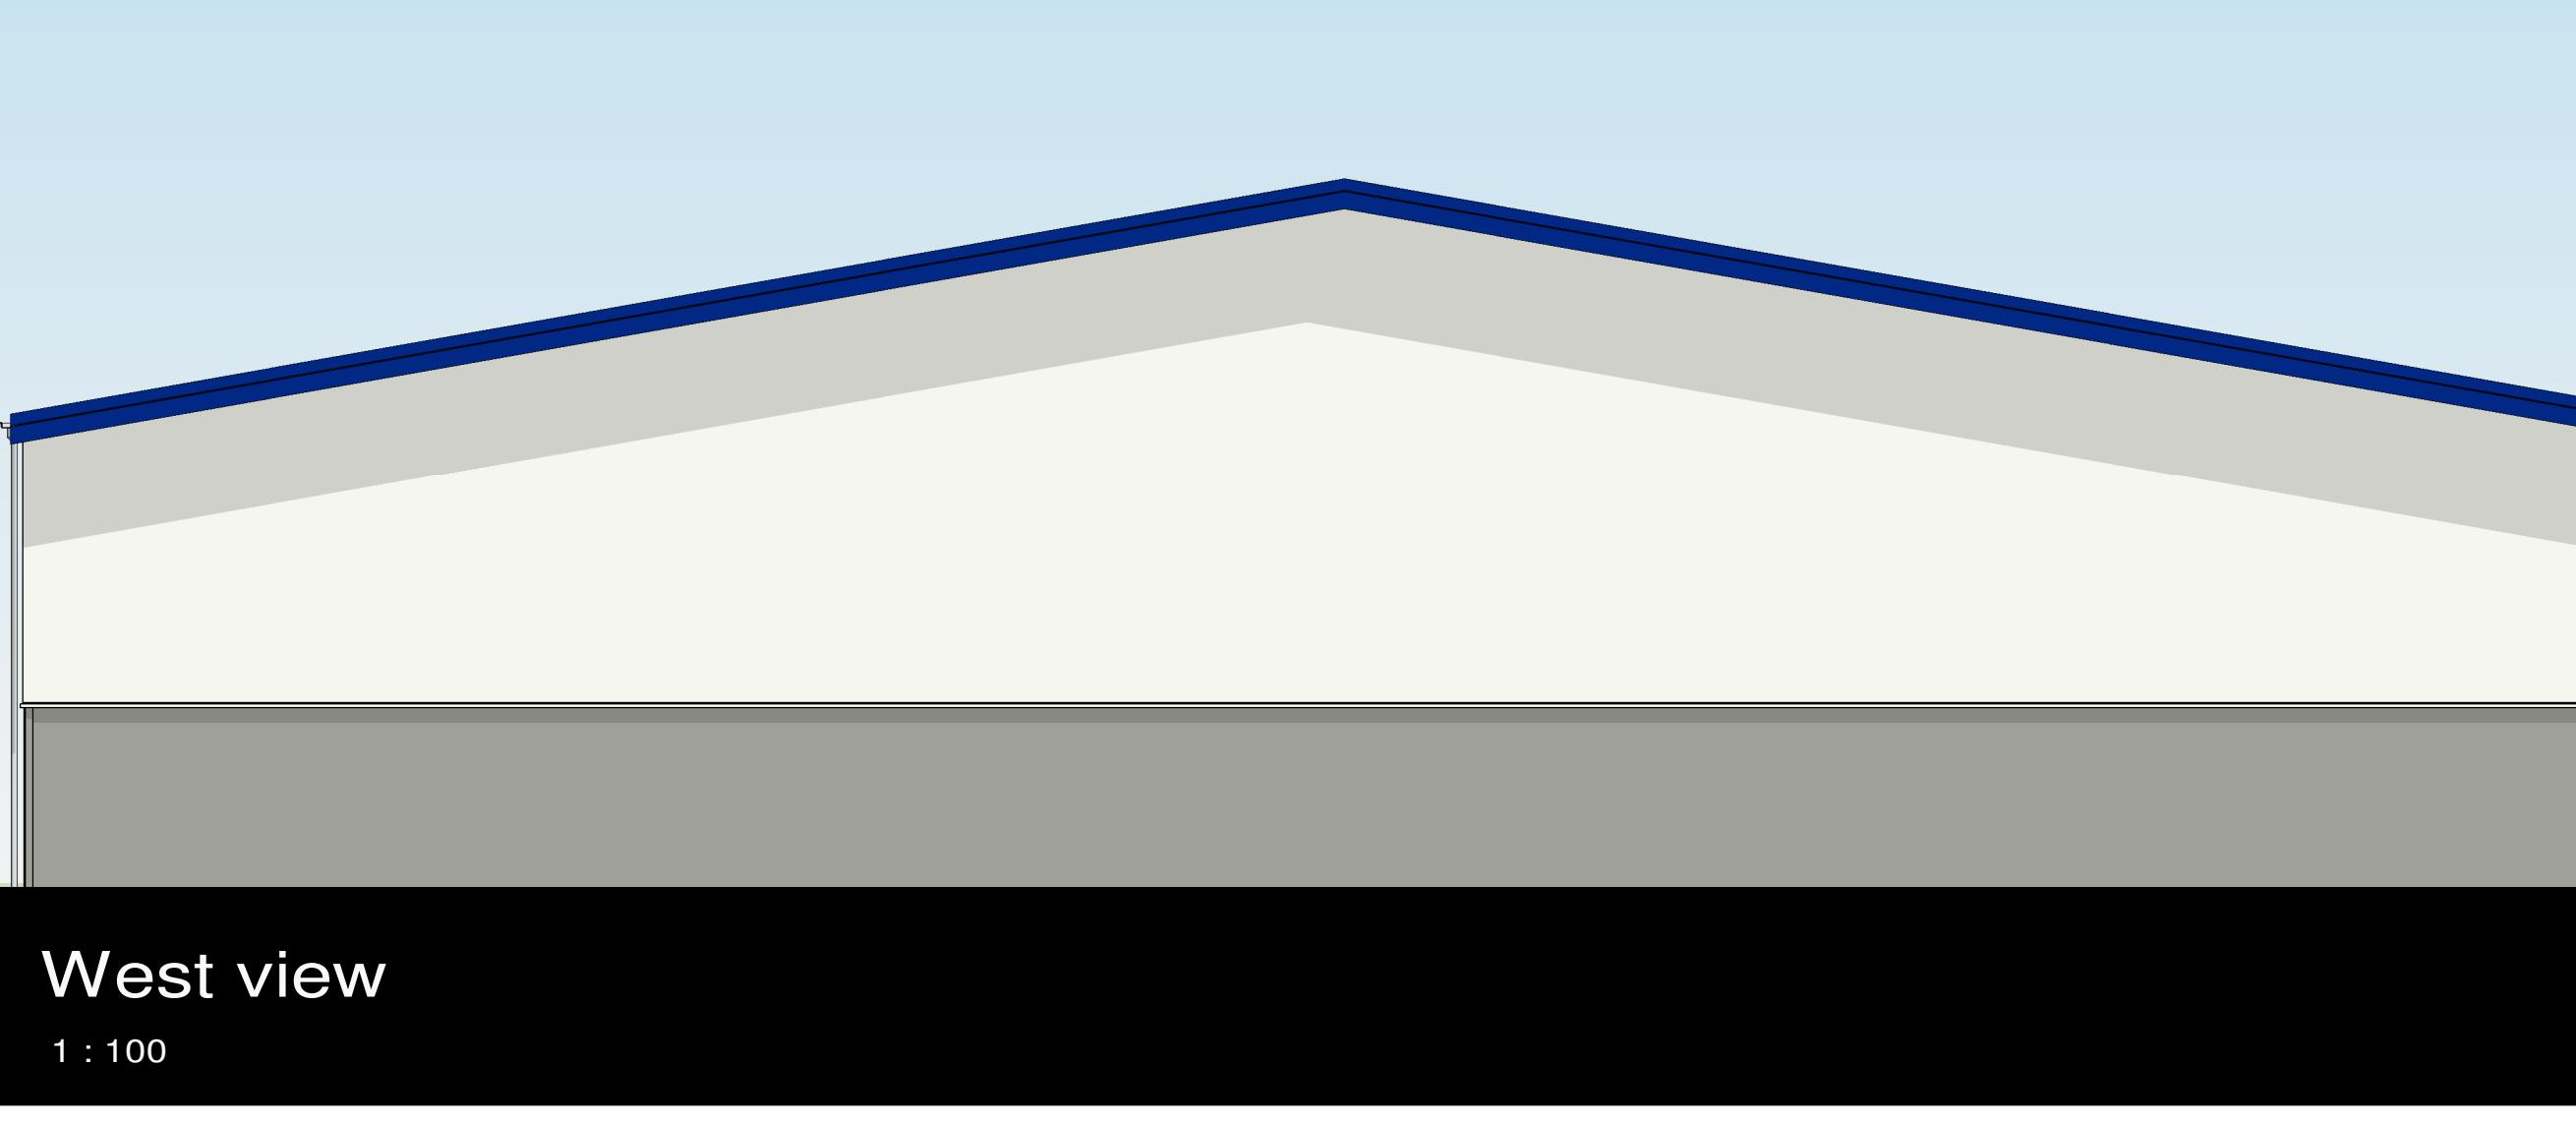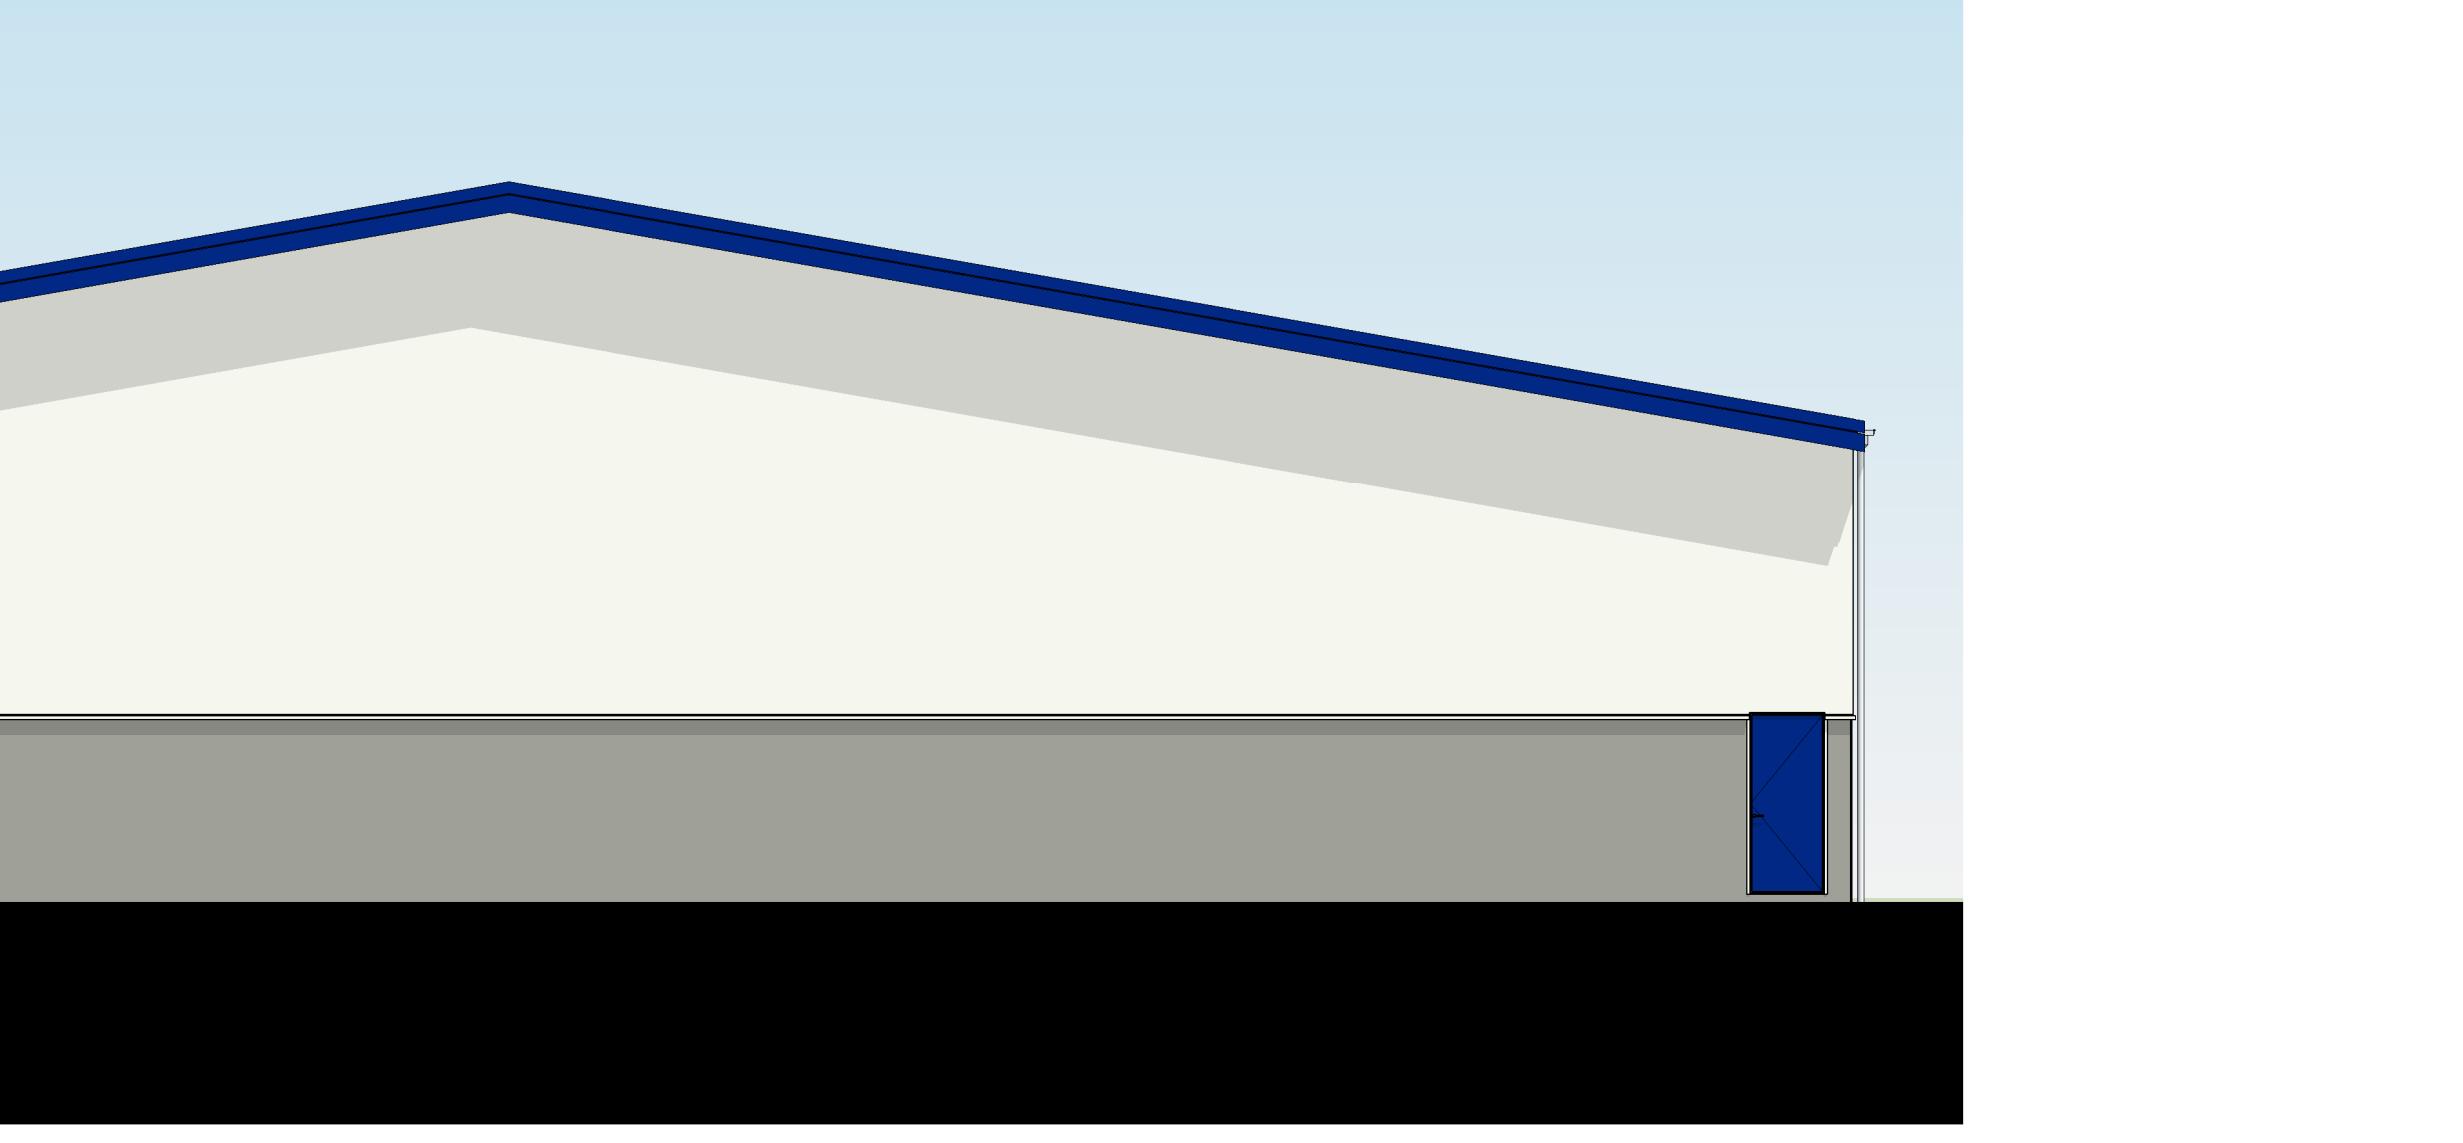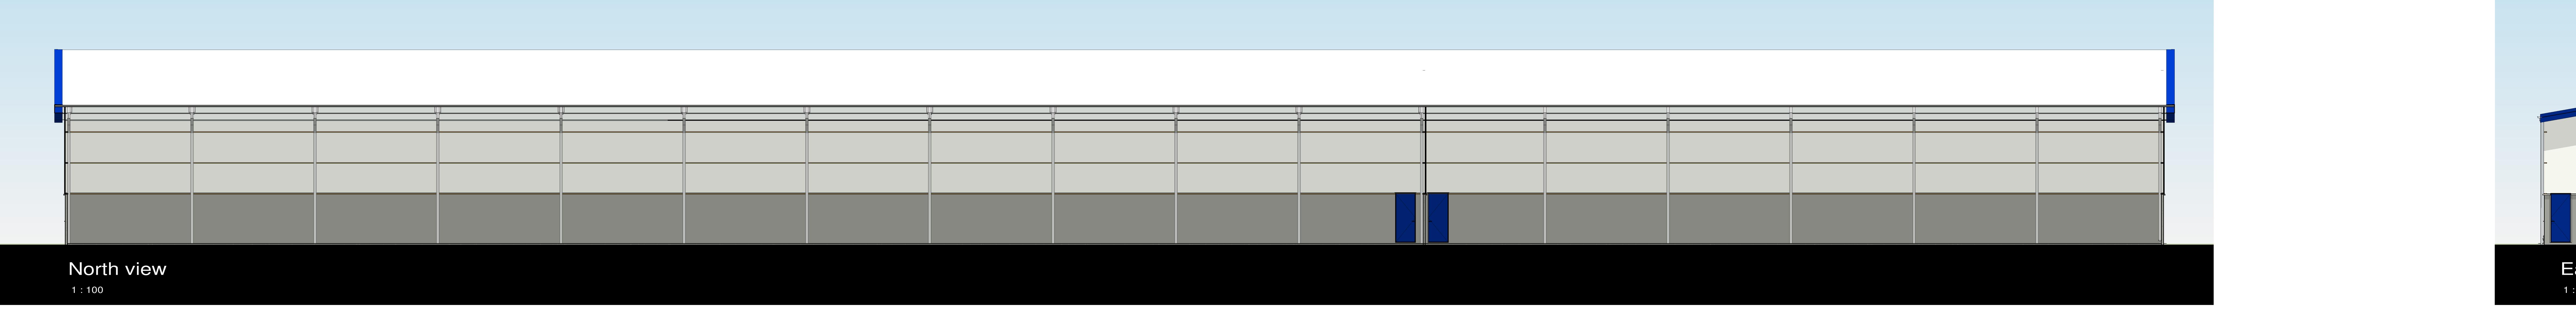

Easy Farming

AGRI PROM

total cow comfort

